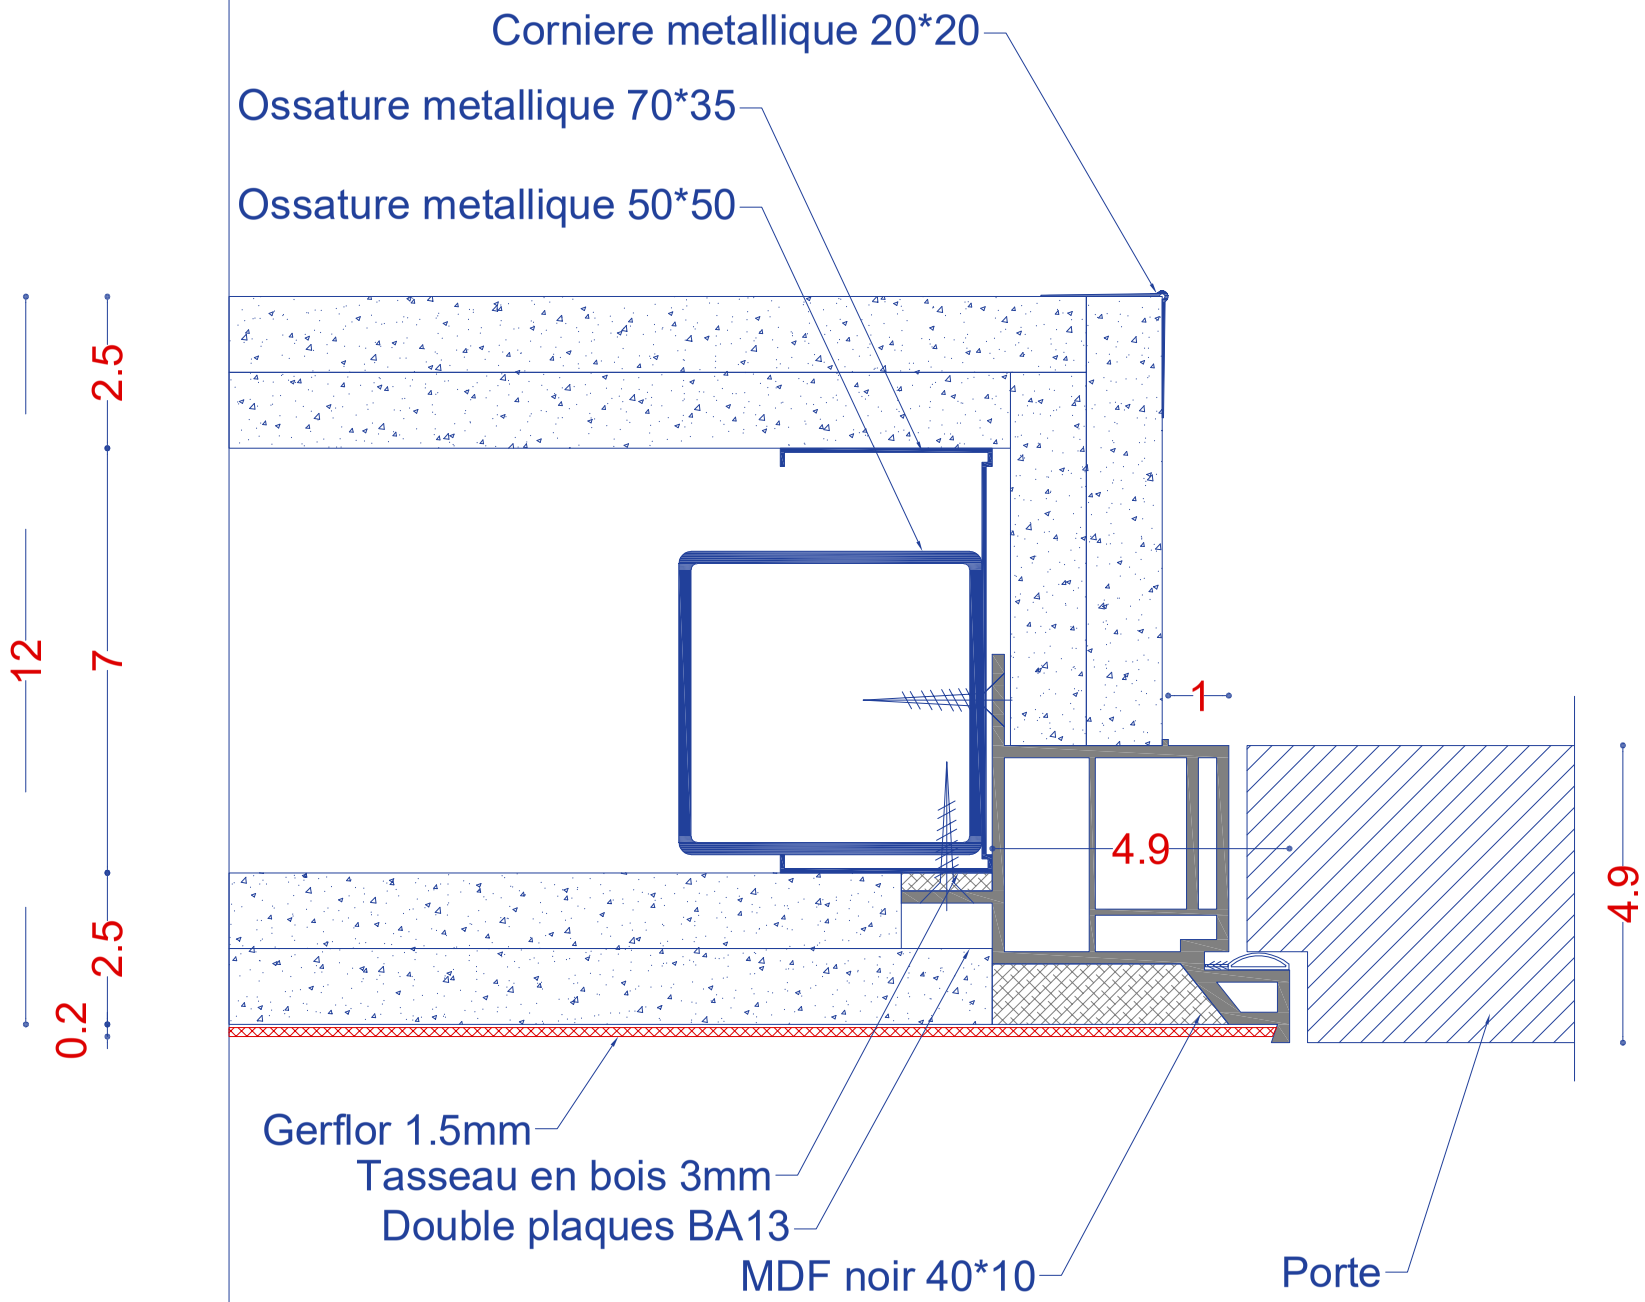

MENUISERIE KHOURY
DEPUIS 1963

(A) DETAIL CADRE ALU SUR BA13

Scale: TO FIT

1. TOUTES LES DIMENSIONS SONT EN CENTIMETRES SAUF INDICATION CONTRAIRE
2. TOUTES LES DIMENSIONS EXISTANTES / LVLS ETC INDIQUÉES SUR DWGS À VÉRIFIER SUR PLACE
3. TOUS LES TRAVAUX DOIVENT ÊTRE EFFECTUÉS CONFORMÉMENT AUX BS PERTINENT CODES DE PRATIQUE ET AUSSI POUR RESPECTER LES EXIGENCES DES AUTORITÉS LOCALES

STATUT:	DESSINE PAR: V K DATE: 21/06/2023	PROJET: HOPITAL GOUMIN	CLIENT: ORANGE	TITRE DE MISE EN PAGE: PLAN ET ELEVATION	NUMERO DU DESSIN: A001	REVISION: BIS 1

Ce document est la propriété de la SOCIETE MK et il ne doit pas être divulgué à des tiers, ni reproduit, sans l'autorisation de la SOCIETE

0 50 100