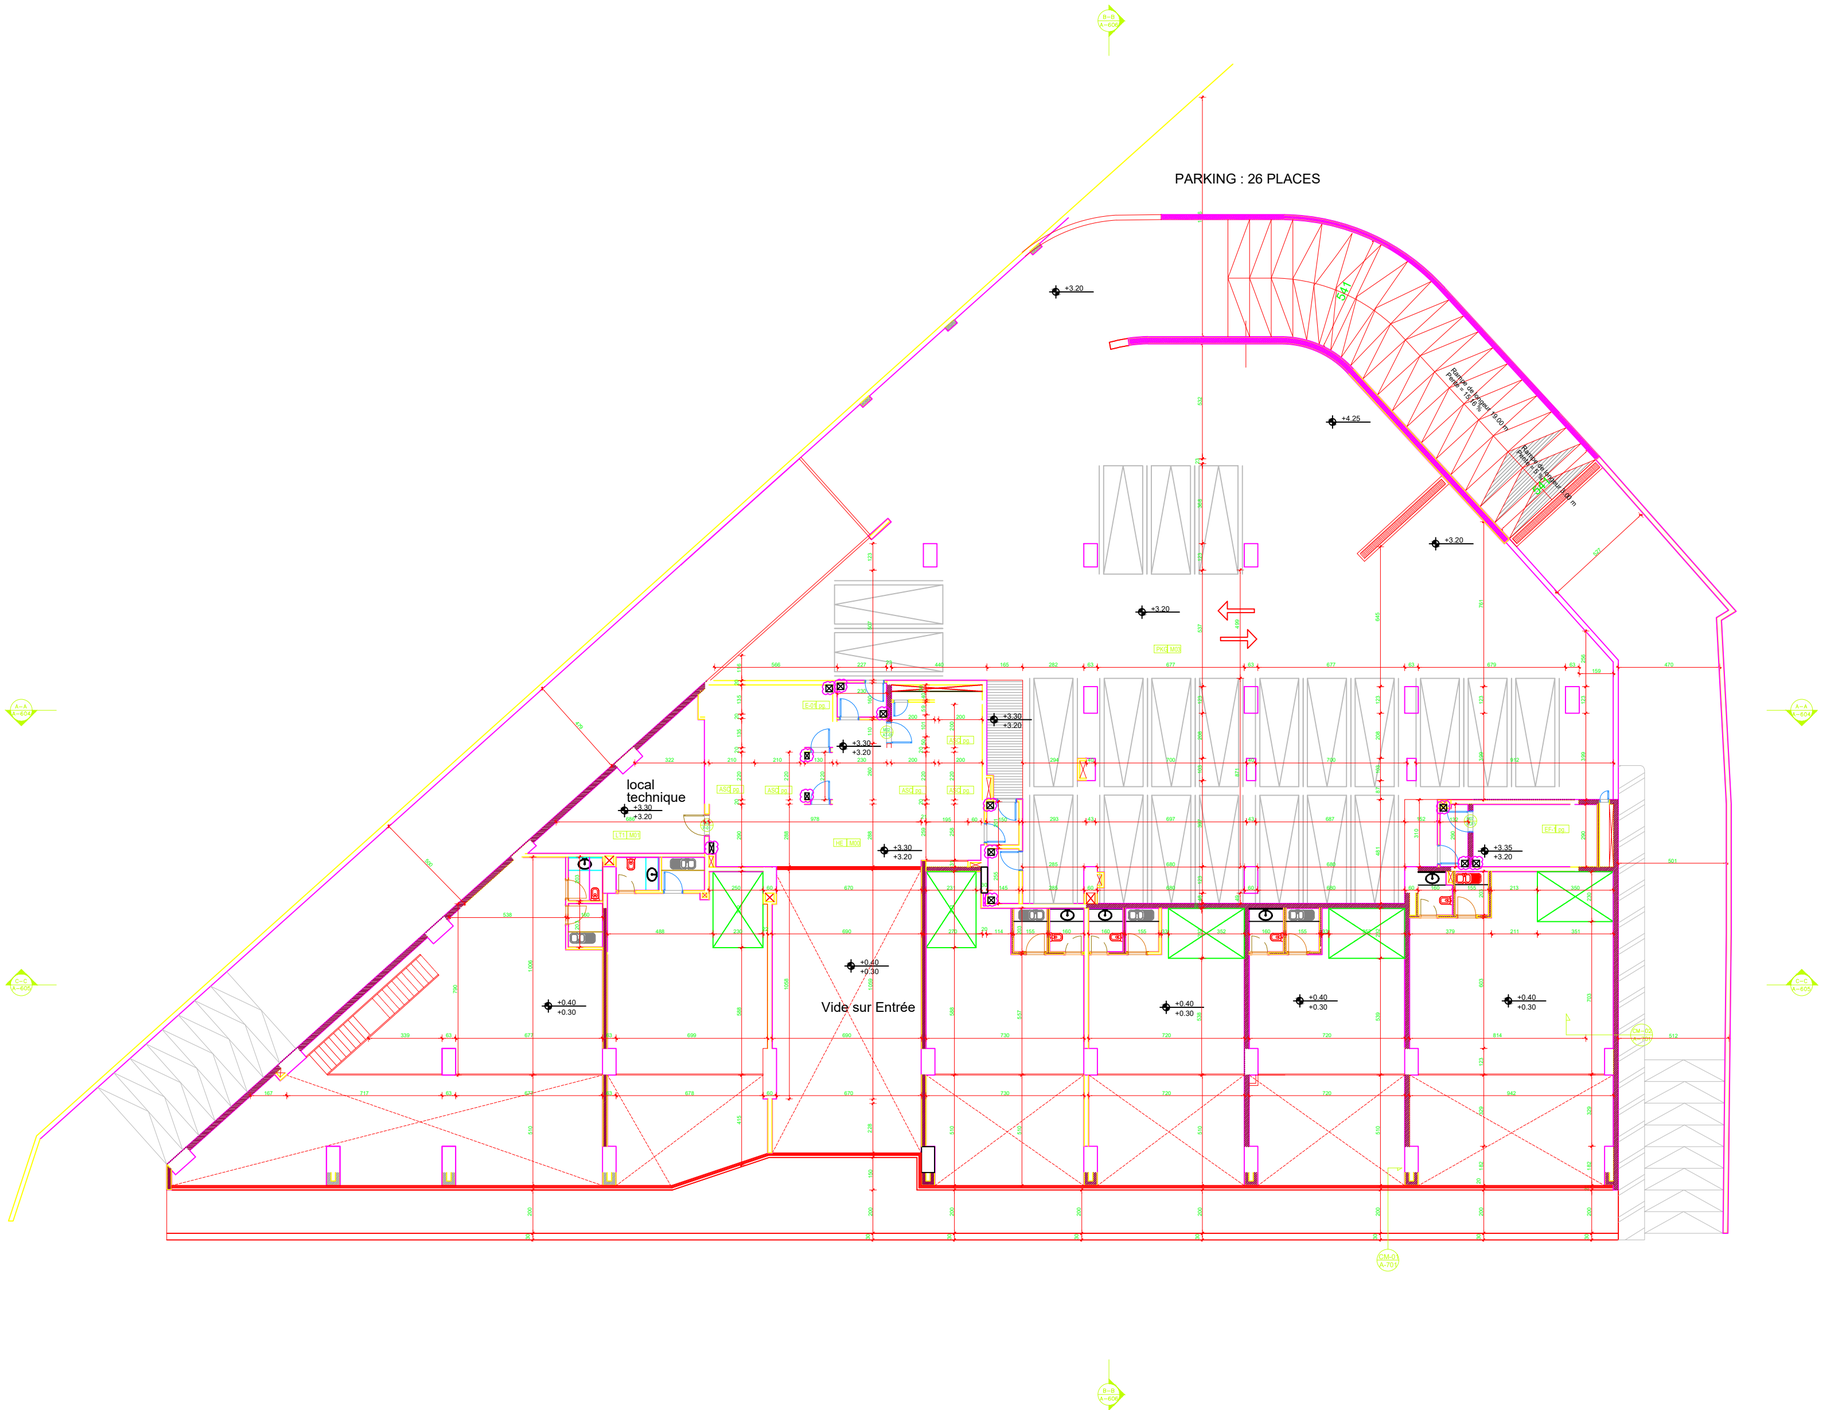

PLAN Mezzanine

PARKING : 26 PLACES

CLIENT

SCI FLAMBOYANT

PROJET

RIVE DROITE
IMMEUBLE BUREAUTIQUE R+12

ARCHITECTE DE CONCEPTION

Lines & Visions

CONSULTANTS STRUCTURAL

Lines & Visions

CONSULTANTS ELEC-MECH

Lines & Visions

ECHELLE

1/200

LE NORD

REVISIONS

Révision 1	R001	17/05/2018
Révision 2	R002	08/06/2018

NO. DELIVRANCE

FICHE D'INFORMATION

DATE: 08/06/2018
N° PROJET: CI160421
DESSINE PAR: Désiré BOGA
VERIFIE PAR: Racha HAMDAR
APPROUVE PAR

PLANS GENERAUX / MEZZANINE

A-102

Pas émis pour construction

.\Jpgs\logo lv.jpg