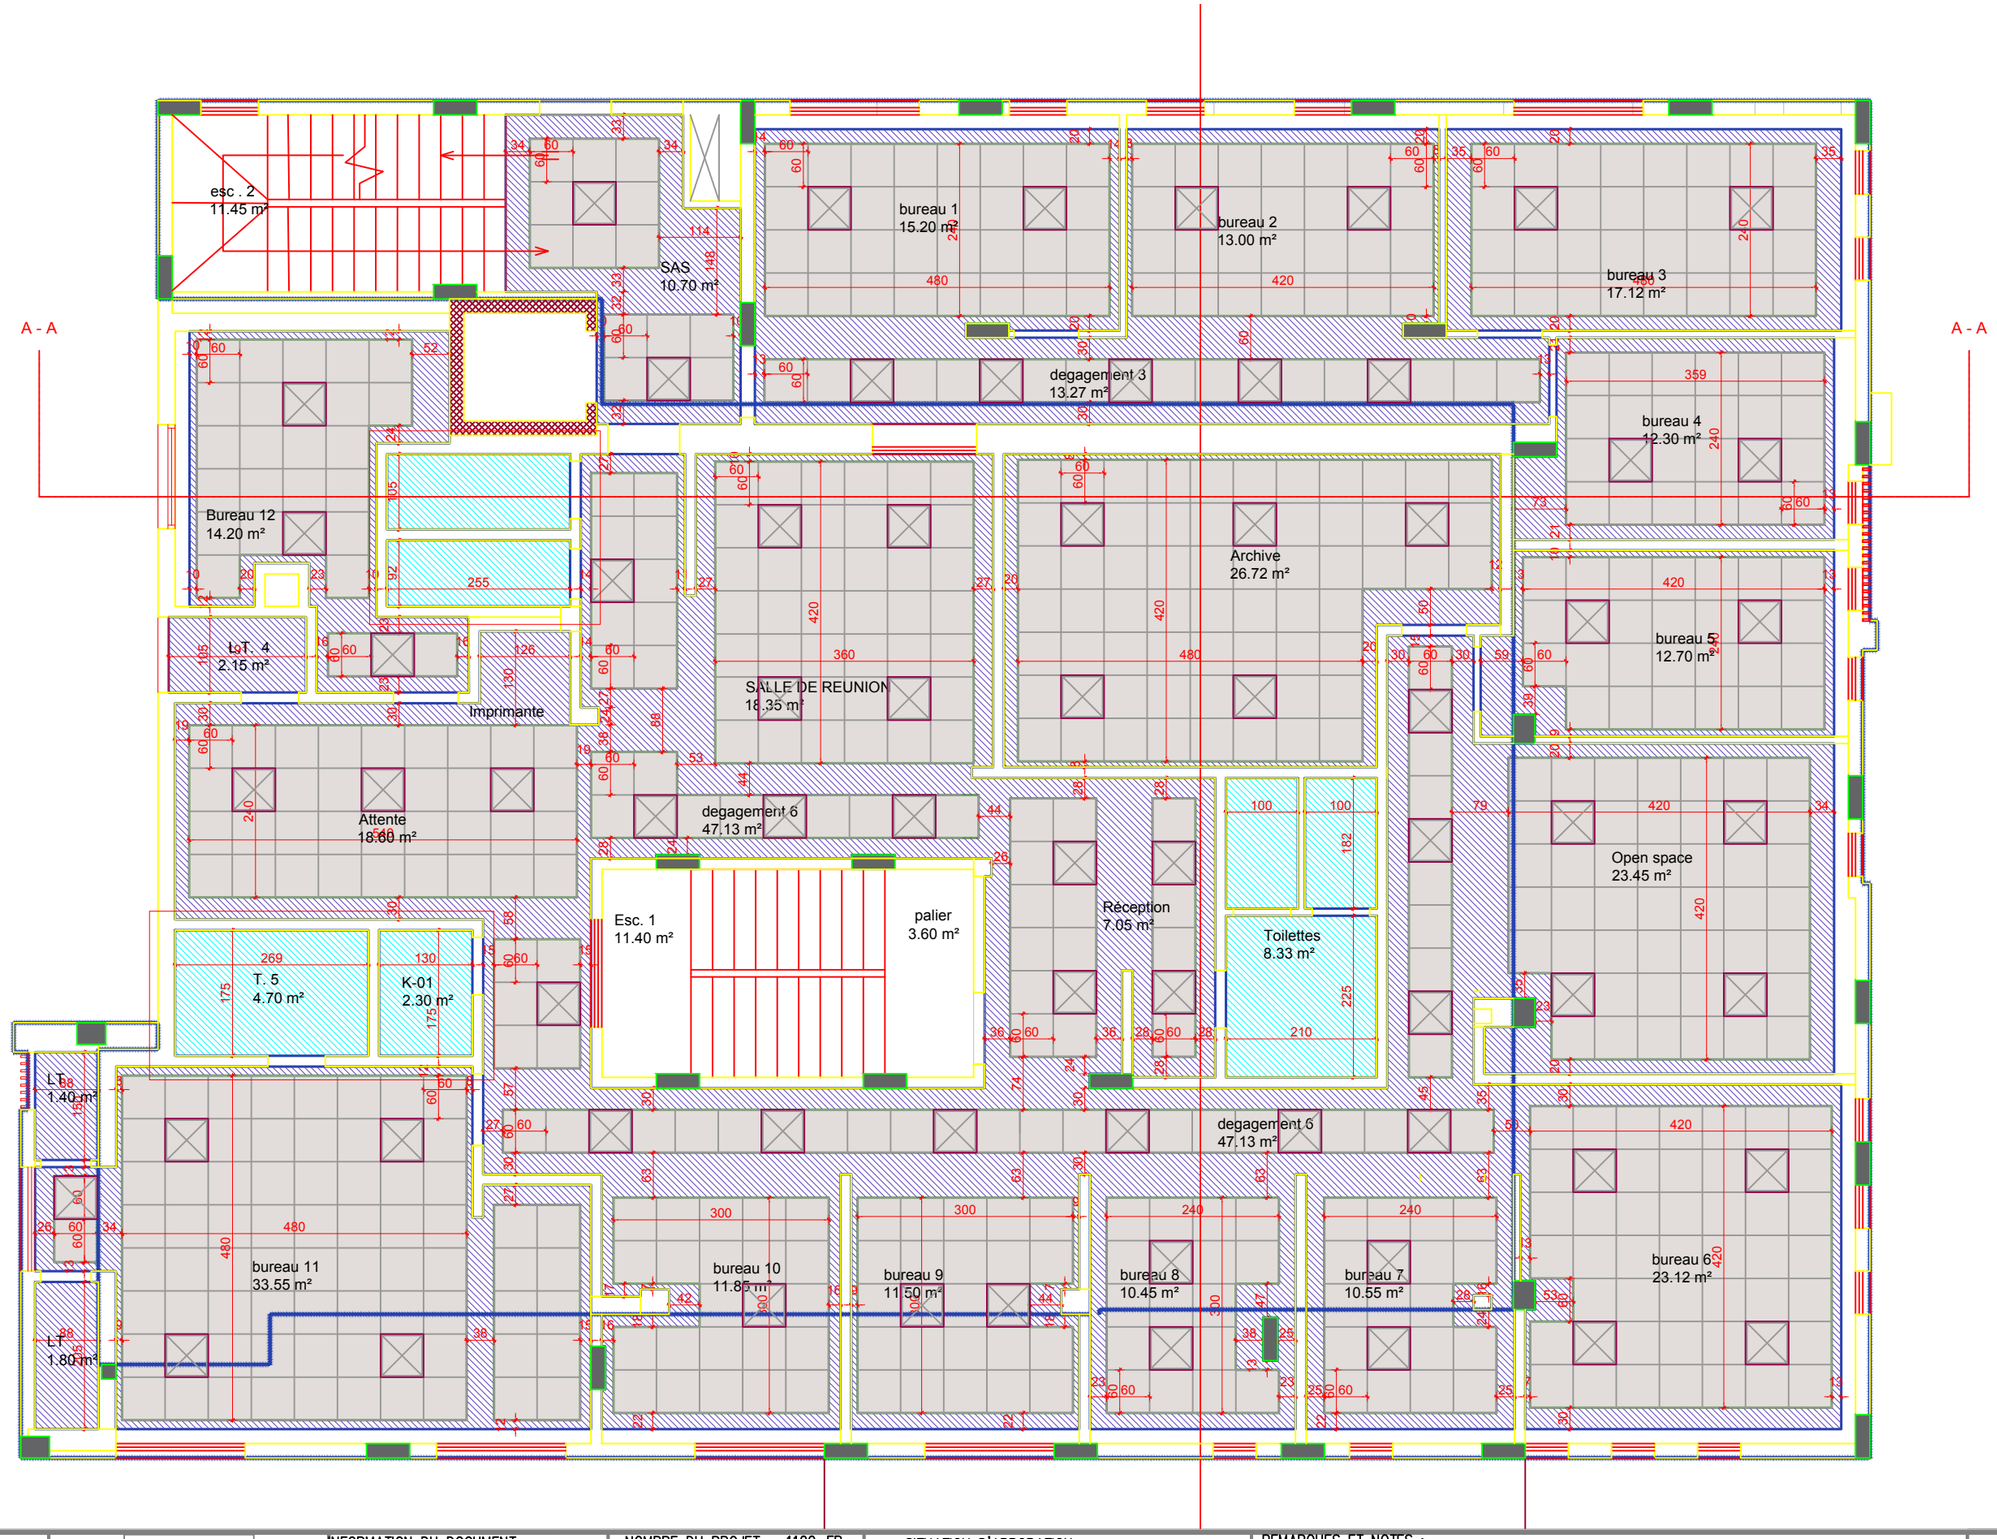

	MAÎTRE D'OUVRAGE DÉLÉGUÉ : 2I-CI SA	INFORMATION DU DOCUMENT	NOMBRE DU PROJET : 1100-FP
		TITRE: PLAN FAUX PLAFOND / 1er ETAGE	DATE: 12 /03/2021
		PLANCHE: 1100 - FP - PA - 002	DESSINÉ PAR:
		ECHELLE: 1/100	VERIFIÉ PAR:
		REVISIONS :	APPROUVÉ PAR:
MAÎTRE D'OUVRAGE : FIDELIS IMMOBILIER	SCI	REV-01 2021 03 12	NORD: ISSUE PURPOSE: STATUS:

SITUATION D'APROBATION :

CODE	DESCRIPTION
A	APPROUVÉ , SANS COMMENTAIRE
B	APPROUVÉ TEL QUE PRÉVU, LES TRAVAUX PEUVENT ÊTRE EXÉCUTER À L'INCORPORATION DES CHANGEMENTS INDIQUÉS.
C	INACCEPTABLE. À RÉVISER ET À REVOIR. LE TRAVAIL NE PEUT PAS ÊTRE SELON CE DOCUMENT.LES REMARQUES SONT ECRITES ET DESSINER SUR LE DOCUMENT

REMARQUES ET NOTES :

Z:\Projets Courants\C1150215-Fidelis\10-Supportlogos\CARTE NEWCUBE_Page_14.jpg

ENTREPRENEUR : NEW CUBE