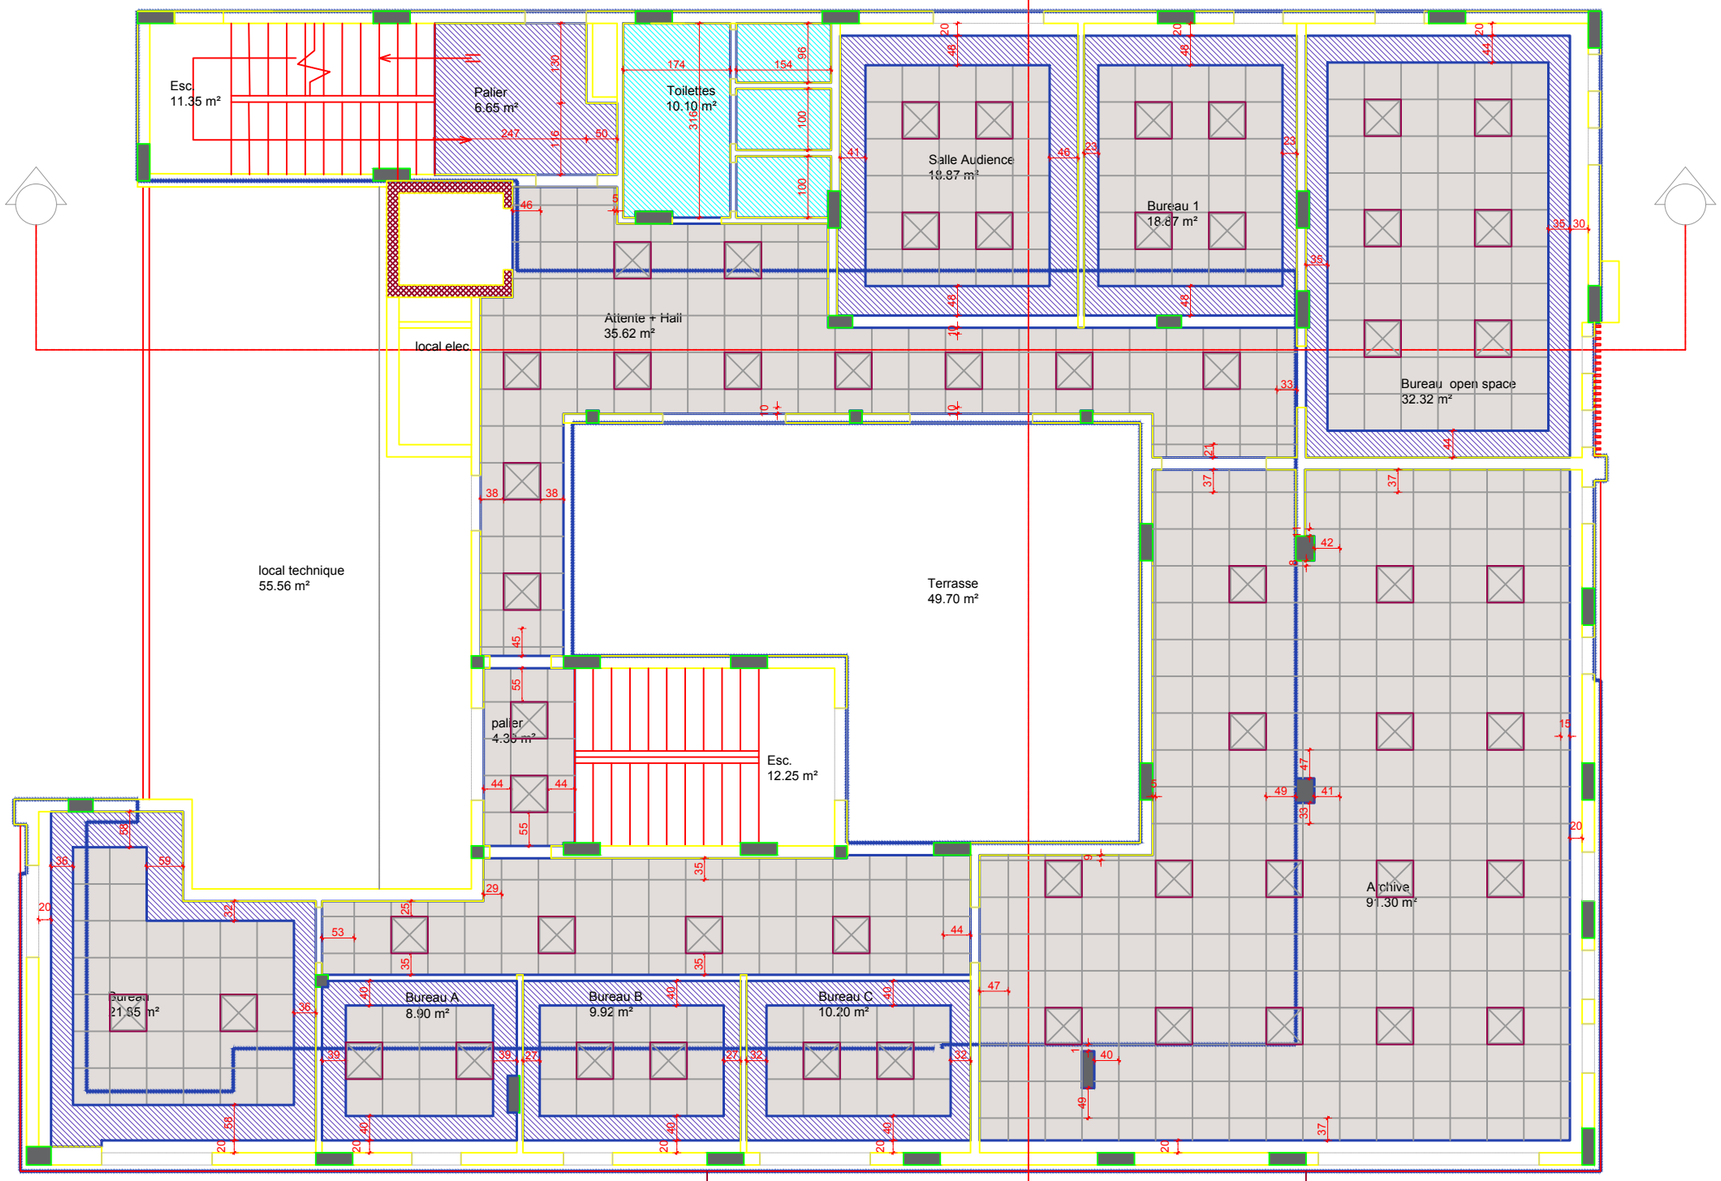


| | | | |
|---|---|---|---|
| MAÎTRE D'OUVRAGE : FIDELIS IMMOBILIER | MAÎTRE D'OUVRAGE DÉLÉGUÉ : 2I-CI SA<br>SCI | INFORMATION DU DOCUMENT<br>TITRE: PLAN FAUX PLAFOND / 2 ème ETAGE<br>PLANCHE: 1100 – FP – PA – 003<br>ECHELLE: 1/100<br>REVISIONS :<br>REV-01 2021 03 12 | NOMBRE DU PROJET : 1100-FP<br>DATE: 12 /03/2021<br>DESSINÉ PAR:<br>VERIFIÉ PAR:<br>APPROUVÉ PAR:<br>NORD: ISSUE PURPOSE: STATUS: |

SITUATION D'APROBATION :

| | CODE | DESCRIPTION |
|---|---|---|
| √ | A | APPROUVÉ , SANS COMMENTAIRE |
| | B | APPROUVÉ TEL QUE PRÉVU, LES TRAVAUX PEUVENT ÊTRE EXÉCUTER À L'INCORPORATION DES CHANGEMENTS INDIQUÉS. |
| | C | INACCEPTABLE. À RÉVISER ET À REVOIR. LE TRAVAIL NE PEUT PAS ÊTRE SELON CE DOCUMENT.LES REMARQUES SONT ECRITES ET DESSINER SUR LE DOCUMENT |

REMARQUES ET NOTES :

Z:\Projets Courants\CI150215-Fidelis\10-Support\logos\CARTE NEWCUBE_Page_14.jpg

ENTREPRENEUR : NEW CUBE