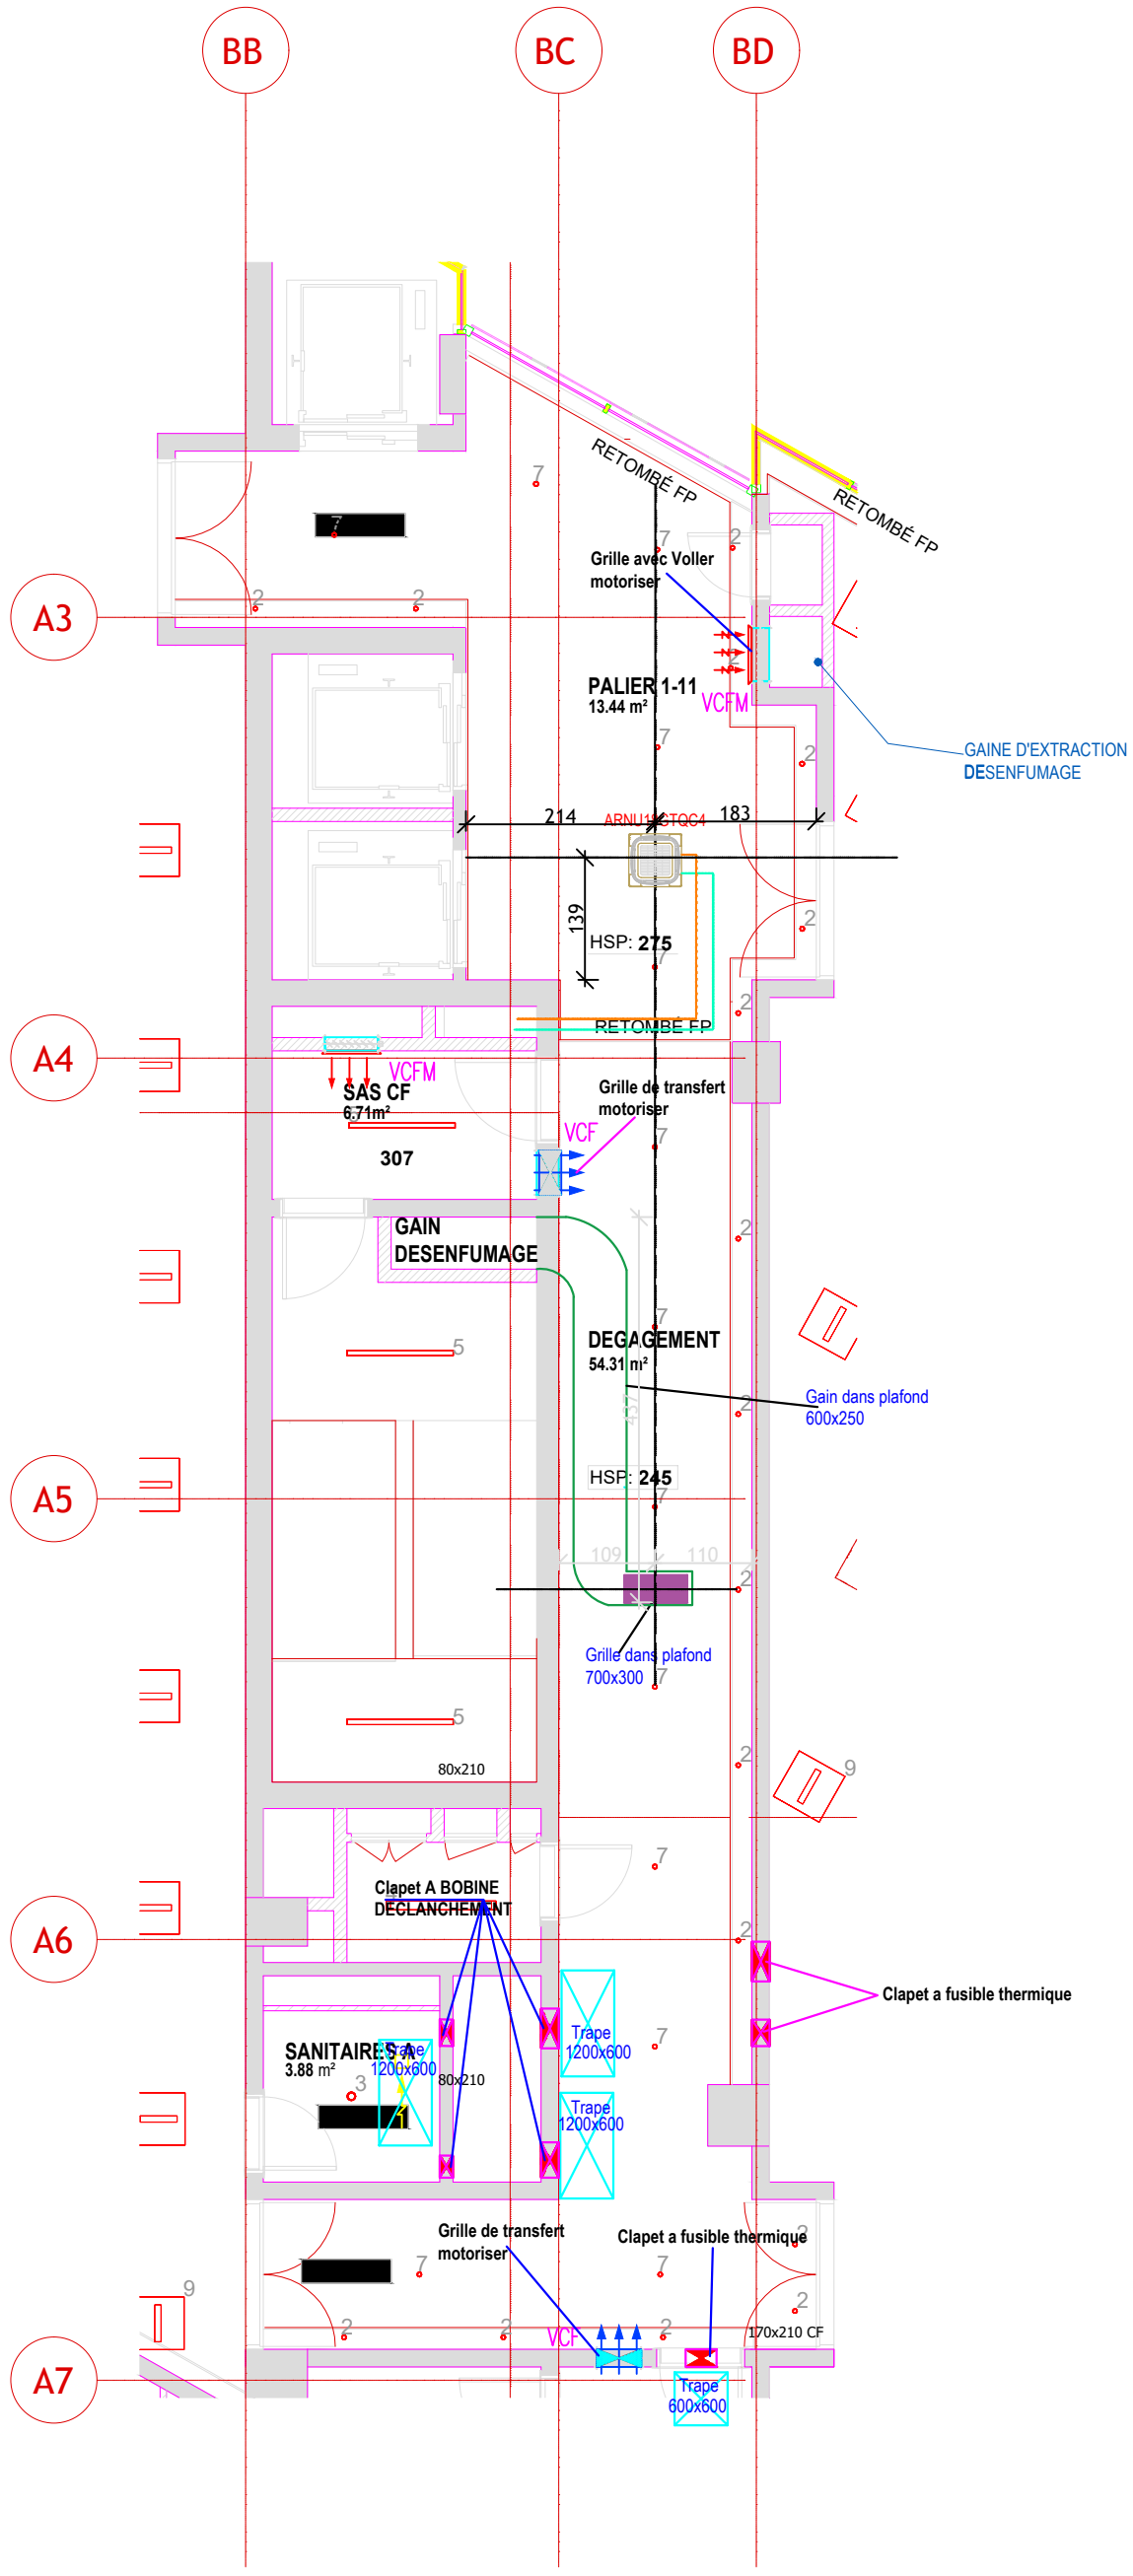
BB
BC
BD
A3
A4
A5
A6
A7
RETOMBÉ FP
RETOMBÉ FP
Grille avec Voller motoriser
PALIER 1-11
13.44 m²
VCFM
GAINE D'EXTRACTION DESENFUMAGE
214
183
139
HSP: 275
RETOMBE FP
VCFM
SAS CF
6.71m²
307
Grille de transfert motoriser
VCF
GAIN DESENFUMAGE
DEGAGEMENT
54.31 m²
Gain dans plafond 600x250
HSP: 245
109
110
Grille dans plafond 700x300
80x210
Clapet A BOBINE DECLANCHEMENT
Clapet a fusible thermique
SANITAIRES
3.88 m²
Trape 1200x600
80x210
Trape 1200x600
Trape 1200x600
Grille de transfert motoriser
Clapet a fusible thermique
VCF
170x210 CF
Trape 600x600