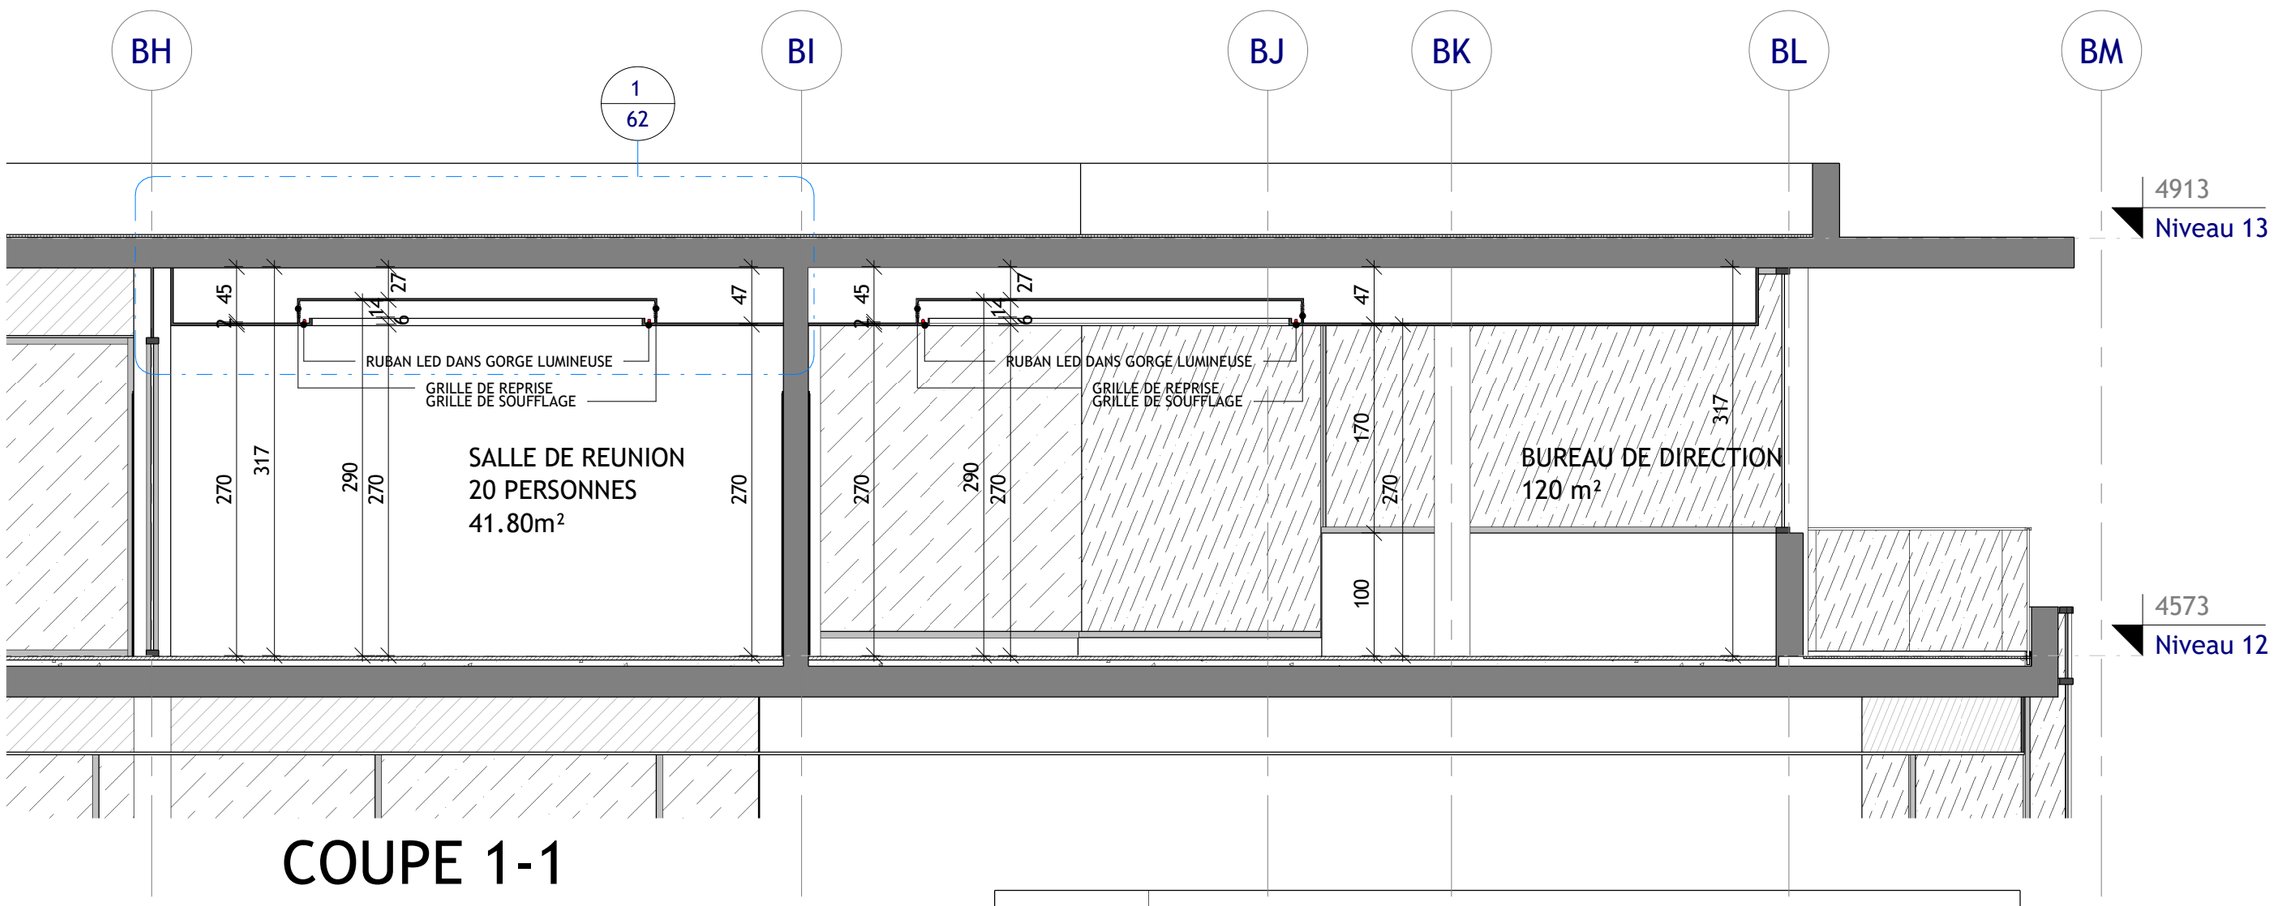

COUPE 1-1

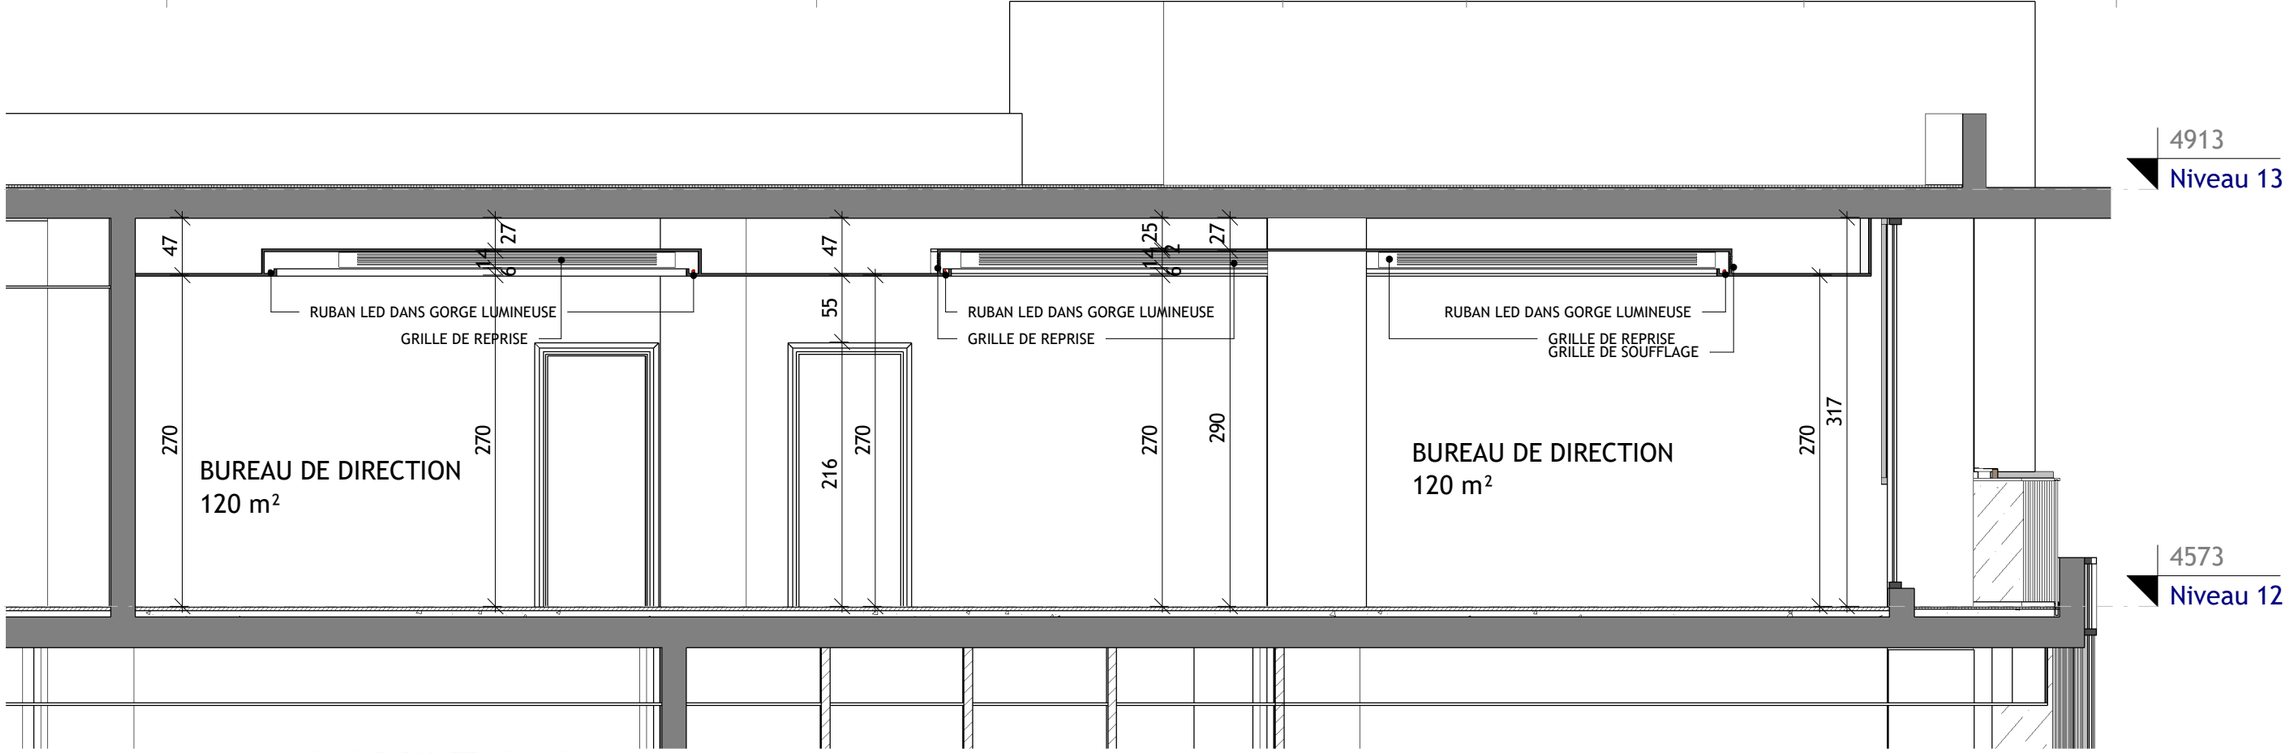

COUPE 2-2

Modification	Ind	Date

DETAILS

DETAILS FP NIVEAU 12
BUREAUX 1/2

Echelle 1 : 50

Plan N° : 61

PALM TOWERS

Affaire THE PALM
Date : 05.11.2020
Chef de JM
Dessiné JM

Architecture Factory
Julien Moukarzel/Architecte d.p.l.g
www.architecture-factory.com
+33.0624308061/+226.09509743

Sauvegardé dans : D:\01.AFFAIRES\01.Architect's Julien\33.The Palm DCE\02.Affaire\02.REVIT\01.Revit Project\2020-11-04\The Palm Towers_20201104_FP12 Bureaux.rvt