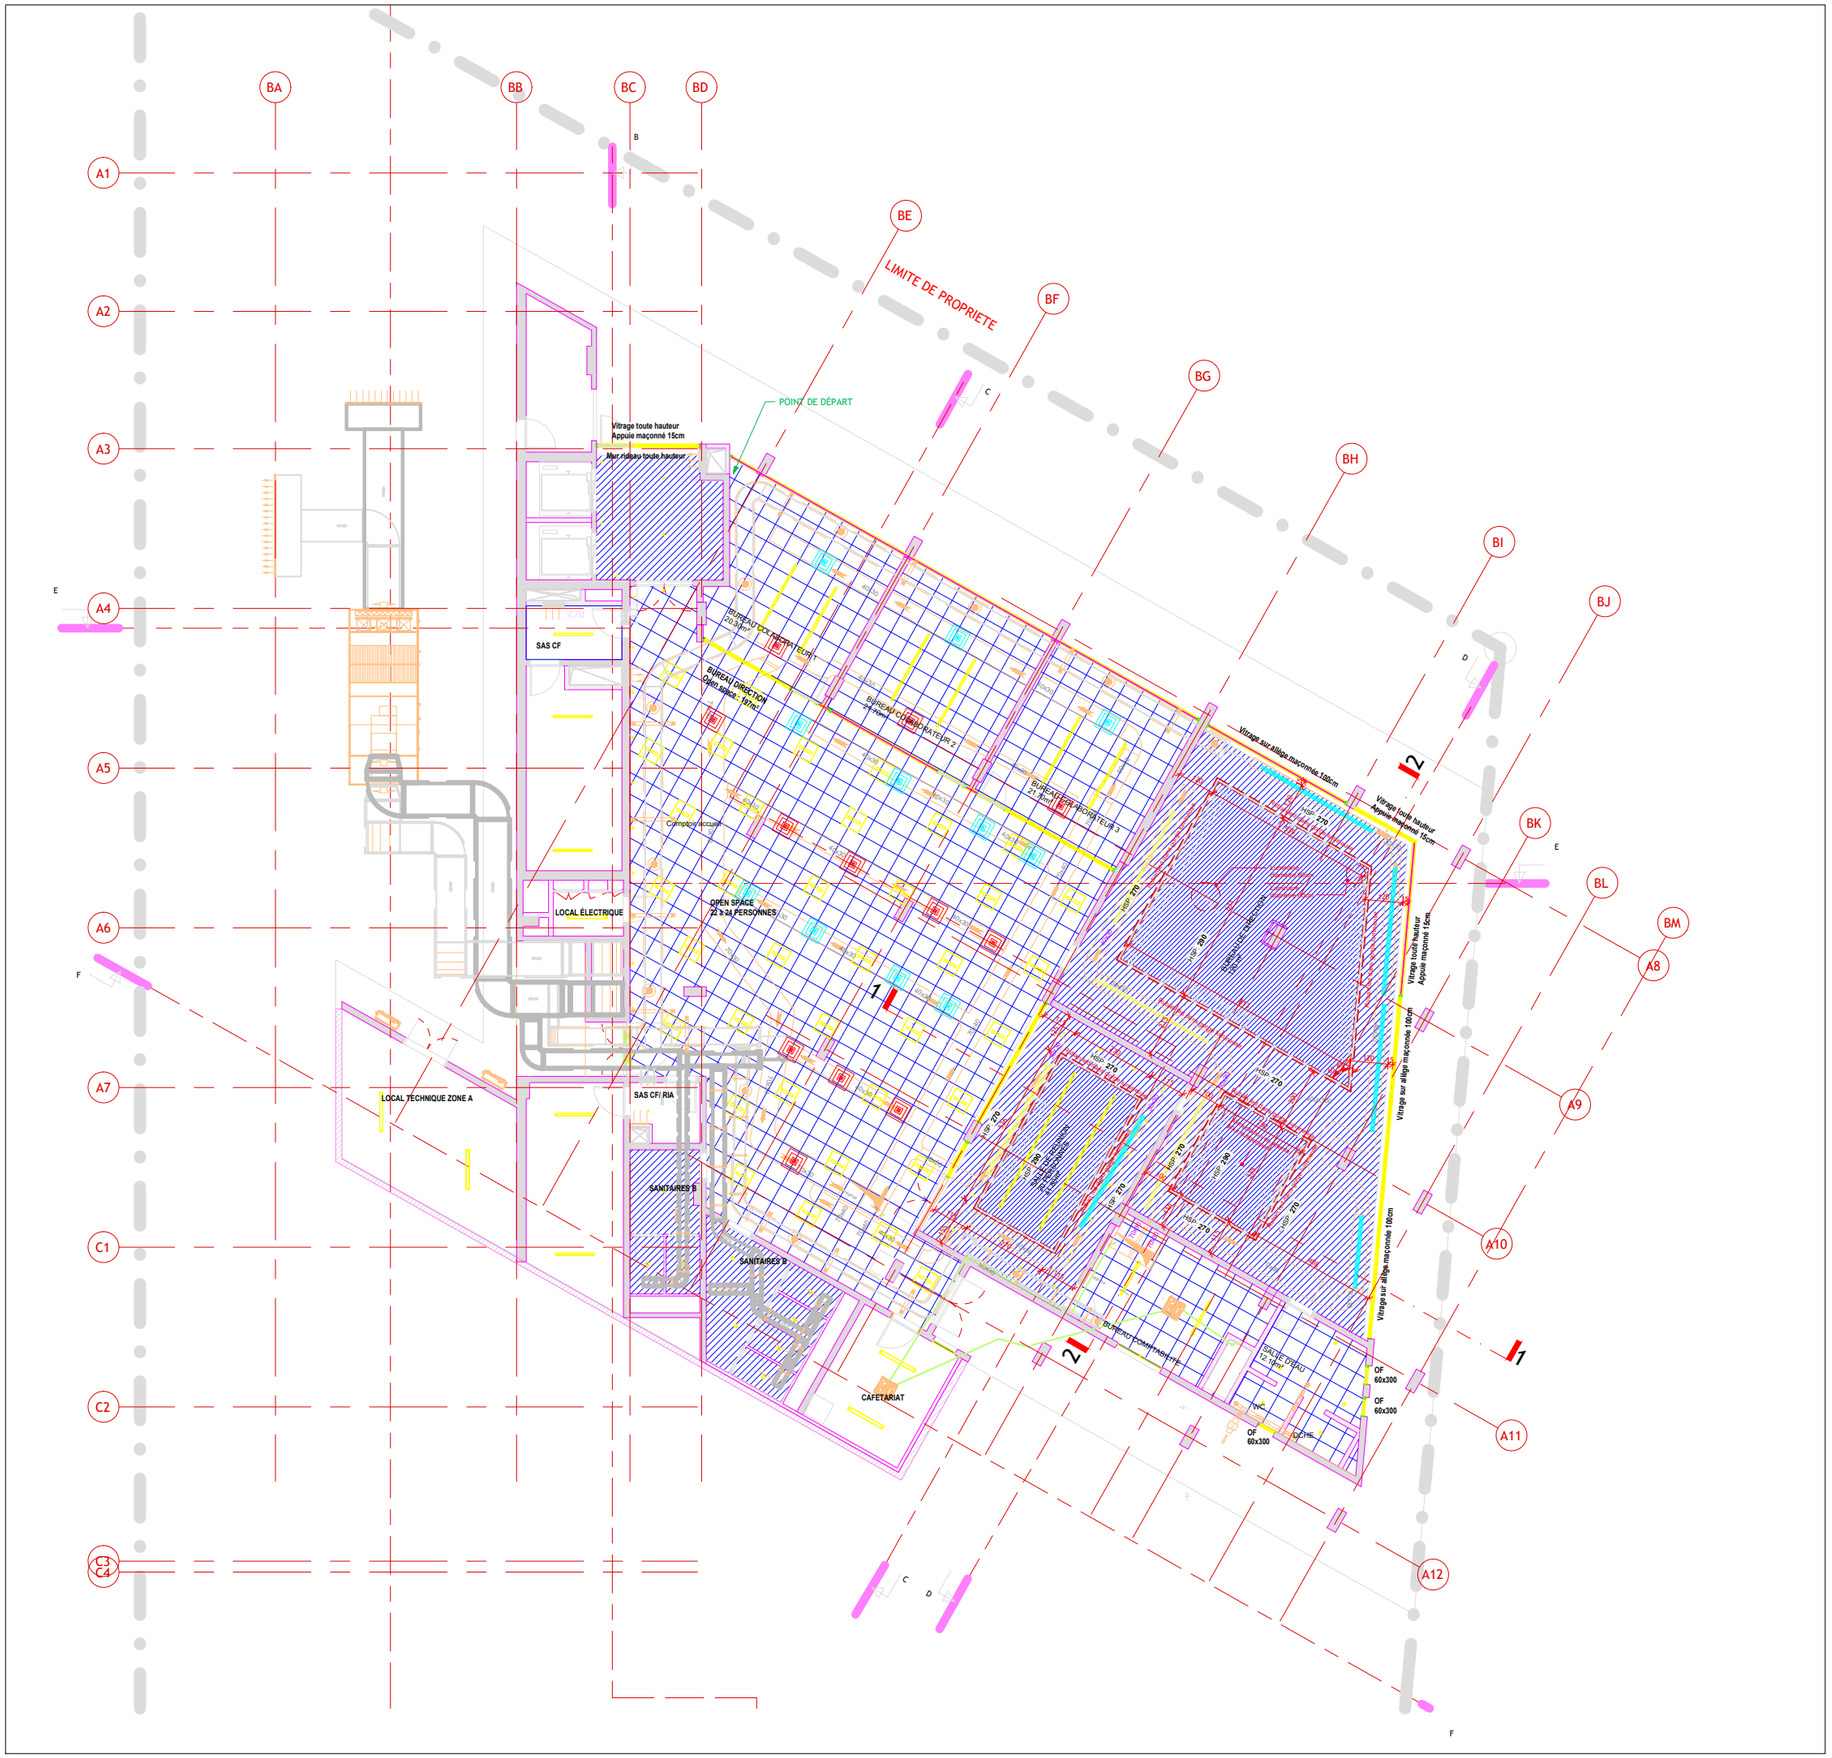

FP placo BA13 + peinture blanche

FP dalle minérale 60x60 couleur blanc

FP panneau acoustique

POP Ring Static Otylight ou équivalent

POP Ring Dynamic Otylight ou équivalent

SUPERNOVA XS RECESSED 330 de Deltalight
(diam. selon réf. plan)

SPOTNIC M10 TRIMLESS O.F.A. de Deltalight ou équivalent

SPOT BASIQUE REF A DÉTERMMINER

SPOT EXTÉRIEUR RÉF. A DÉTERMINER

APPLIQUE MURALE RÉF. A DÉTERMINER

APPLIQUE MURALE EXT. RÉF. A DÉTERMINER

Dalle LED 60x60 cm

REGLETTE FLUORESCENTE OU PLAFONNIER ÉTANCHE
A POSER SOUS DALLE

APPLIQUE TYPE REGLETTE LED SDB

RUBAN LED

PROJECTEUR fixé sur poteau, éclaire sous face des panneaux acoustique

Point lumineux (Cables en attente pour suspension)

TE Tableau électrique

DP Détecteur de présence

Interrupteur simple HT axe 110 cm

Interrupteur double

Va et vient

Va et vient double

Commande ouverture volet roulant - Ht 1.10m

Alimentation en attente pour volet roulant , unité climatiseur et hotte cuisine

Prise de courant - 16 A + terre - Ht 0.30m (sauf indication contraire)

Prise de courant - 16 A + terre - Ht 1.20m

Prise de courant étanche type PLEXO - 16 A + terre

Bloc type M1 : 2ou3 prises - 1 TV - 1 RJ45 + 1 téléphone si besoin

Prise de courant - 16 A + terre - encastré au sol

Récepteur vidéophone /
Interphone

Note: Les luminaires situés dans les pièces d'eau et/ou à l'extérieur devront être étanches