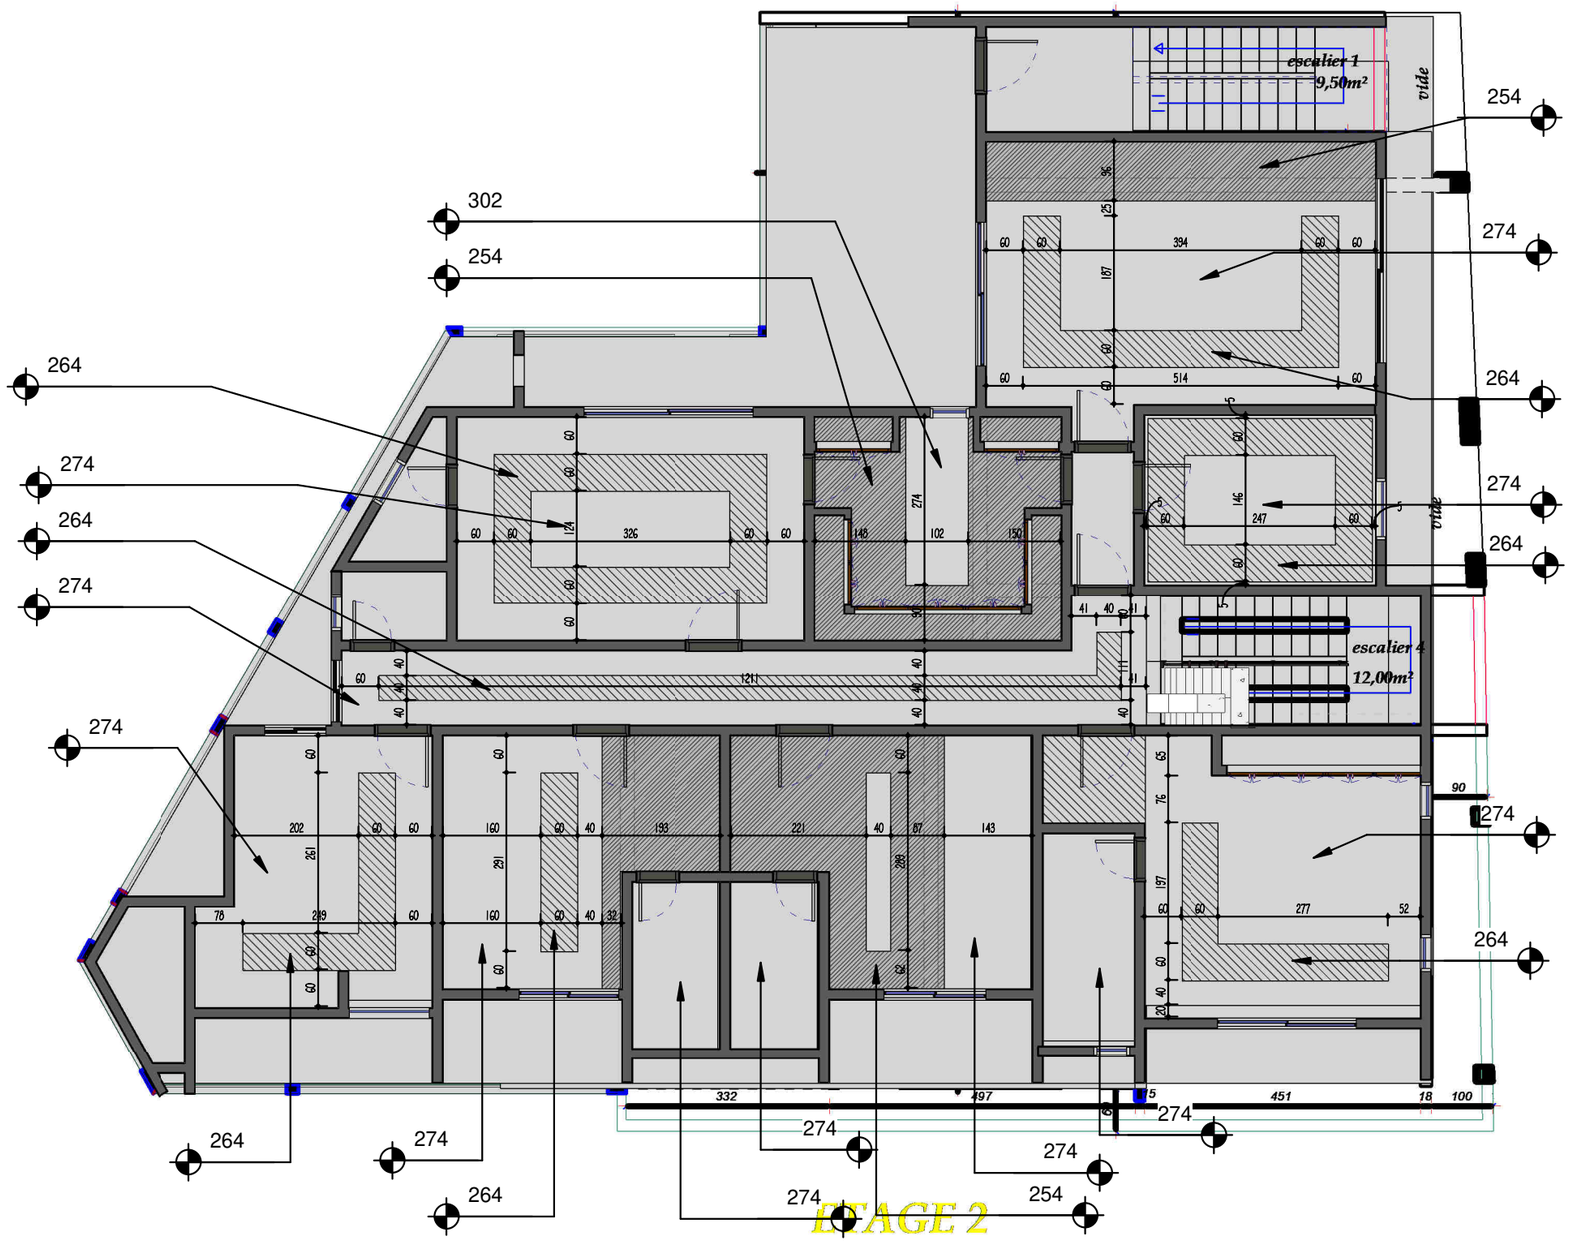


AFFAIRE:

MAITRE D'OEUVRE

EGARD

CHEF DE PROJET

ARTHUR EHOUNOUD

DESSIN

AUTEUR

PROJET

VILLA FOFIE

| AP | AP |
|---|---|
| D | S |

ECHELLE

1 : 100

PLAN N°

B 02

IMPRESSION

29/04/2021 20:06:15

PLAN PLAFOND ETAGE

MAITRE OUVRAGE

Lu et approuvé

MAITRE OEUVRE

Lu et approuvé

CE PROJET EST UNE PROPRIÉTÉ D'EGARD-ARCHITECTURE DESIGN. IL NE DOIT ÊTRE NI REPRODUIT NI MODIFIÉ SANS L'APPROBATION DU MAÎTRE D'OEUVRE. TOUTES MODIFICATIONS APPORTÉES AVEC OU SANS L'ACCORD DU MAÎTRE D'OEUVRE SUR LE PLAN OU SUR LE CHANTIER FERONT L'OBJET D'UN DEVIS SUPPLEMENTAIRE DONC FACTURÉES

COCODY-II PLTX-LAS PALMAS (CITE 81000) BÂT K P124)
06 BP 535 ABJ 06, TEL: 22 0148 75 / 22 42 06 48
FAX: 22 42 05 66, EMAIL: INFOS@EGARD-CI.COM

Sauvegardé dans: F:\PROJET EGARD 2020\4- VILLAS\FOFIE\VILLA FOFIE APS 6.rte

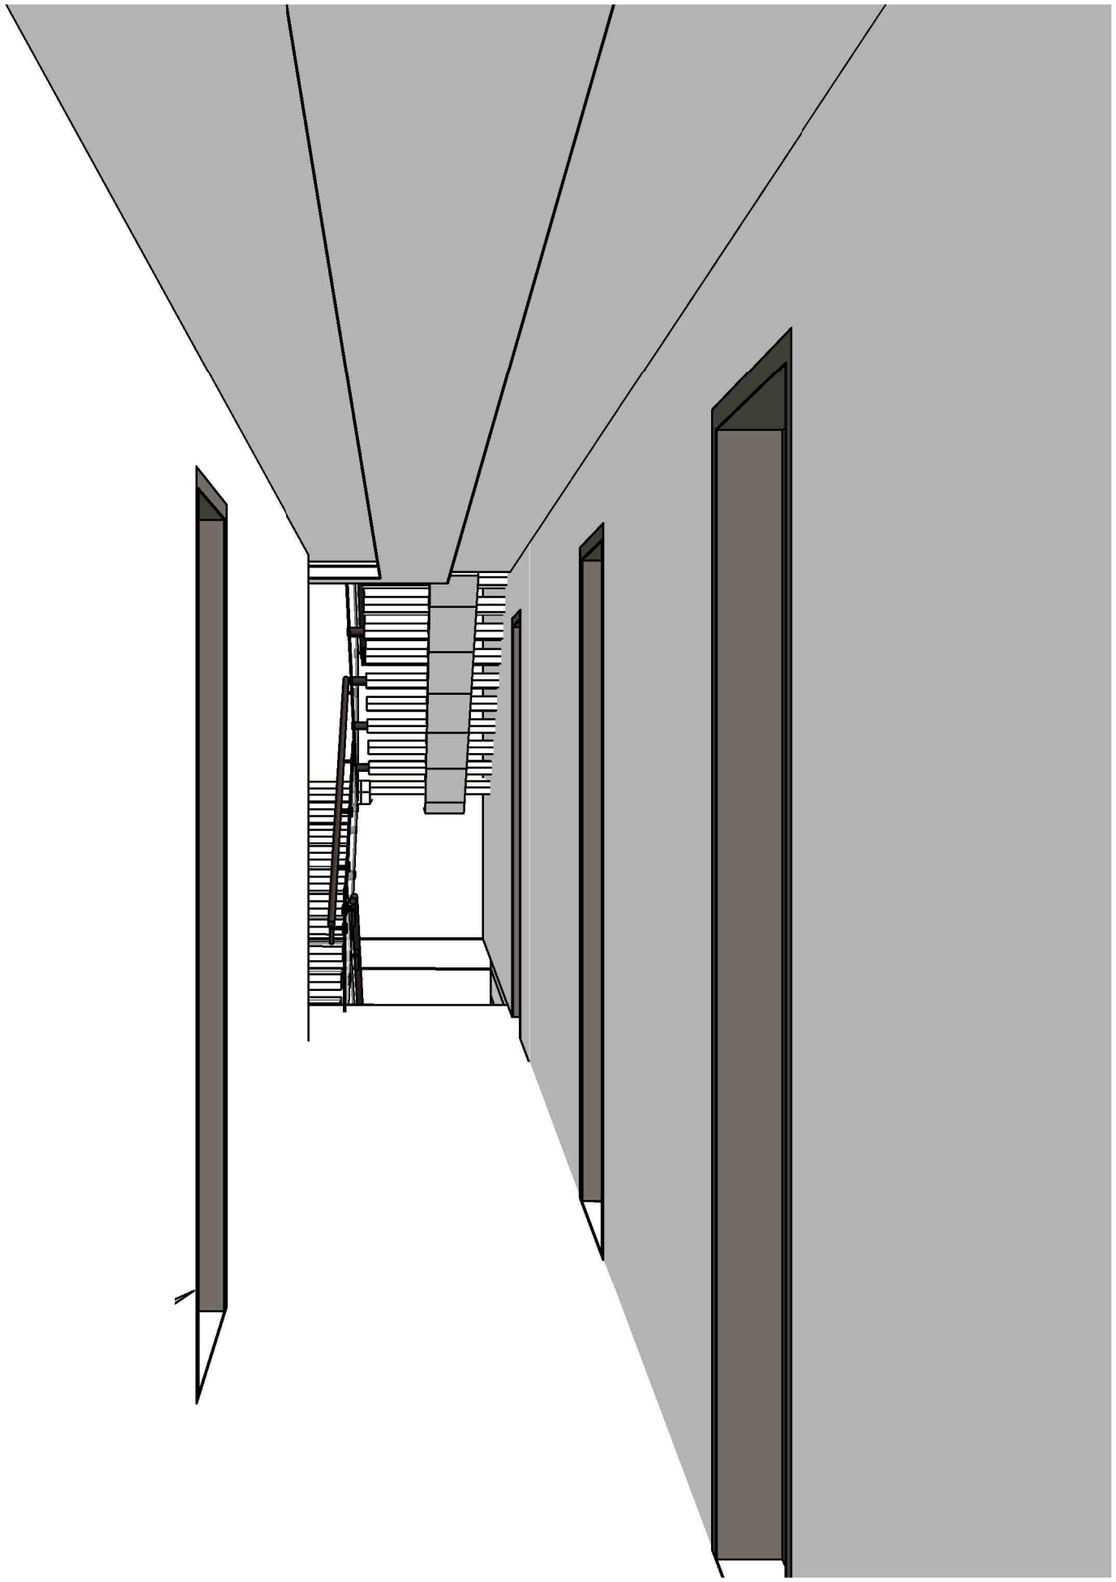

AFFAIRE:

MAITRE D'OEUVRE

EGARD

CHEF DE PROJET

ARTHUR EHOUNOUD

DESSIN

AUTEUR

PROJET

VILLA FOFIE

| AP | AP |
|---|---|
| D | S |

ECHELLE

PLAN N°

B 02.1

IMPRESSION

29/04/2021 20:06:16

VUE 3D COULOIR ETAGE

MAITRE OUVRAGE

Lu et approuvé

MAITRE OEUVRE

Lu et approuvé

Ce projet est une propriété d'EGARD-Architecture Design. Il ne doit être ni reproduit ni modifié sans l'approbation du maître d'oeuvre. Toutes modifications apportées avec ou sans l'accord du Maître d'oeuvre sur le plan ou sur le chantier feront l'objet d'un devis supplementaire donc facturées

COCODY-II PLTX-LAB PALMAB (CITE SICOGI BÂT K P124)
06 BP 535 ABJ 06, TEL: 22 0148 75 / 22 42 06 48
FAX: 22 42 05 66, EMAIL: INFOS@EGARD-CI.COM

Sauvegardé dans: F:\PROJET EGARD 2020\4- VILLAS\FOFIE\VILLA FOFIE APS 6.rte

AFFAIRE:

MAITRE D'OEUVRE

EGARD

CHEF DE PROJET

ARTHUR EHOUNOUD

DESSIN

AUTEUR

PROJET

VILLA FOFIE

| AP | AP |
|---|---|
| D | S |

ECHELLE

PLAN N°

B 02.2

IMPRESSION

29/04/2021 20:06:19

VUE 3D SALON FAMILLIAL

MAITRE OUVRAGE

Lu et approuvé

MAITRE OEUVRE

Lu et approuvé

Ce projet est une propriété d'EGARD-Architecture Design. Il ne doit être ni reproduit ni modifié sans l'approbation du maître d'oeuvre. Toutes modifications apportées avec ou sans l'accord du Maître d'oeuvre sur le plan ou sur le chantier feront l'objet d'un devis supplementaire donc facturées

COCODY-II PLTX-LAS PALMAS (CITE SICOGI BÂT K P124)
06 BP 535 ABJ 06, TEL: 22 0148 75 / 22 42 06 48
FAX: 22 42 05 66, EMAIL: infos@egard-ci.com

Sauvegardé dans: F:\PROJET EGARD 2020\4- VILLAS\FOFIE\VILLA FOFIE APS 6.rte

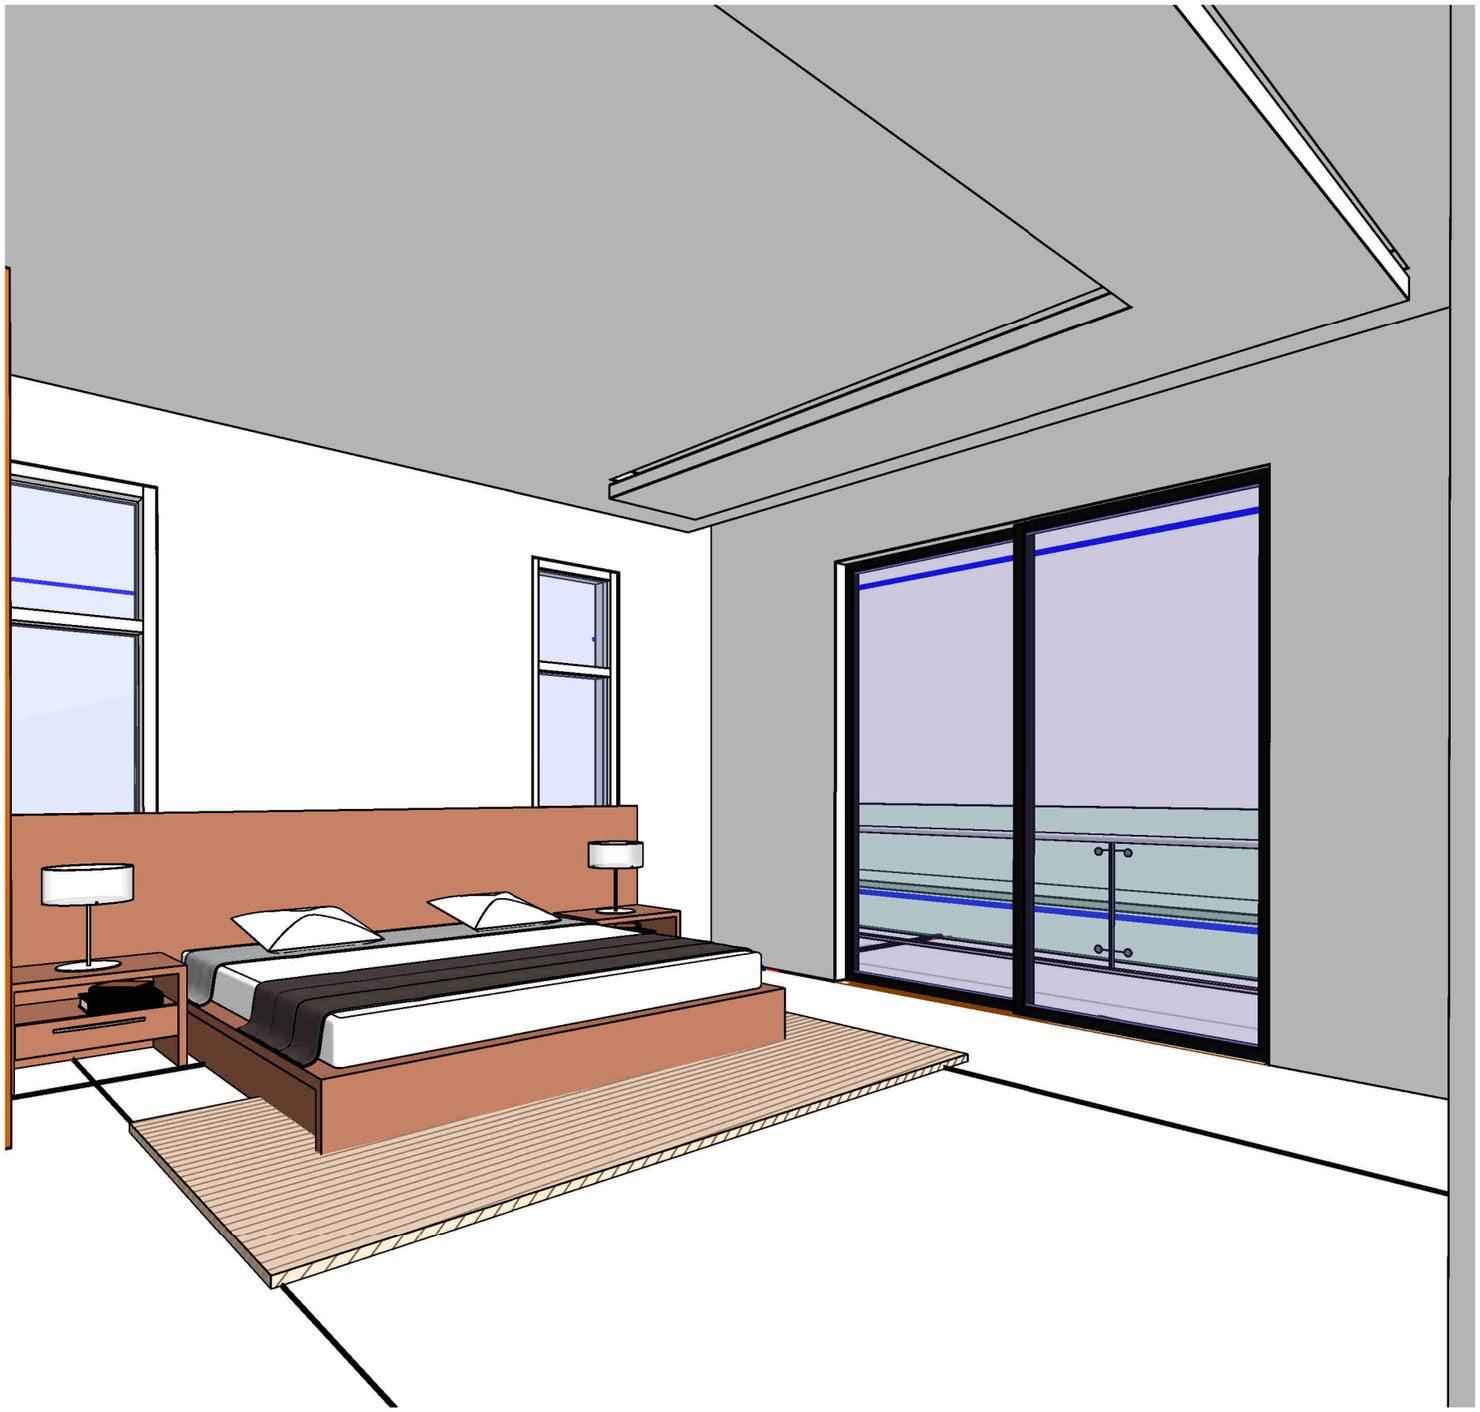

1 Vue 3D 20
Ech :

AFFAIRE:

MAITRE D'OEUVRE
EGARD

CHEF DE PROJET
ARTHUR EHOUNOUD

DESSIN
AUTEUR

PROJET
VILLA FOFIE

| AP | AP |
|---|---|
| D | S |

ECHELLE

PLAN N°
B 02.3

IMPRESSION
29/04/2021 20:06:20

VUE 3D CH SECONDAIRE

MAITRE OUVRAGE
Lu et approuvé

MAITRE OEUVRE
Lu et approuvé

Ce projet est une propriété d'EGARD-Architecture Design. Il ne doit être ni reproduit ni modifié sans l'approbation du maître d'oeuvre. Toutes modifications apportées avec ou sans l'accord du Maître d'oeuvre sur le plan ou sur le chantier feront l'objet d'un devis supplementaire donc facturées

COCODY-II PLTX-LAB PALMAB (CITE SICOGI BÂT K P124)
06 BP 535 ABJ 06, TEL: 22 0148 75 / 22 42 06 48
FAX: 22 42 05 66, EMAIL: INFOS@EGARD-CI.COM

Sauvegardé dans: F:\PROJET EGARD 2020\4- VILLAS\FOFIE\VILLA FOFIE APS 6.rte

AFFAIRE:

MAITRE D'OEUVRE

EGARD

CHEF DE PROJET

ARTHUR EHOUNOUD

DESSIN

AUTEUR

PROJET

VILLA FOFIE

| AP | AP |
|---|---|
| D | S |

ECHELLE

PLAN N°

B 02.4

IMPRESSION

29/04/2021 20:06:21

VUE 3D CH PRIN

MAITRE OUVRAGE

Lu et approuvé

MAITRE OEUVRE

Lu et approuvé

Ce projet est une propriété d'EGARD-Architecture Design. Il ne doit être ni reproduit ni modifié sans l'approbation du maître d'oeuvre. Toutes modifications apportées avec ou sans l'accord du Maître d'oeuvre sur le plan ou sur le chantier feront l'objet d'un devis supplementaire donc facturées

COCODY-II PLTX-LAB PALMAB (CITE SICOGI BÂT K P124)
06 BP 535 ABJ 06, TEL: 22 01 48 78 / 22 42 06 48
FAX: 22 42 05 66, EMAIL: infos@egard-ci.com

Sauvegardé dans: F:\PROJET EGARD 2020\4- VILLAS\FOFIE\VILLA FOFIE APS 6.rte

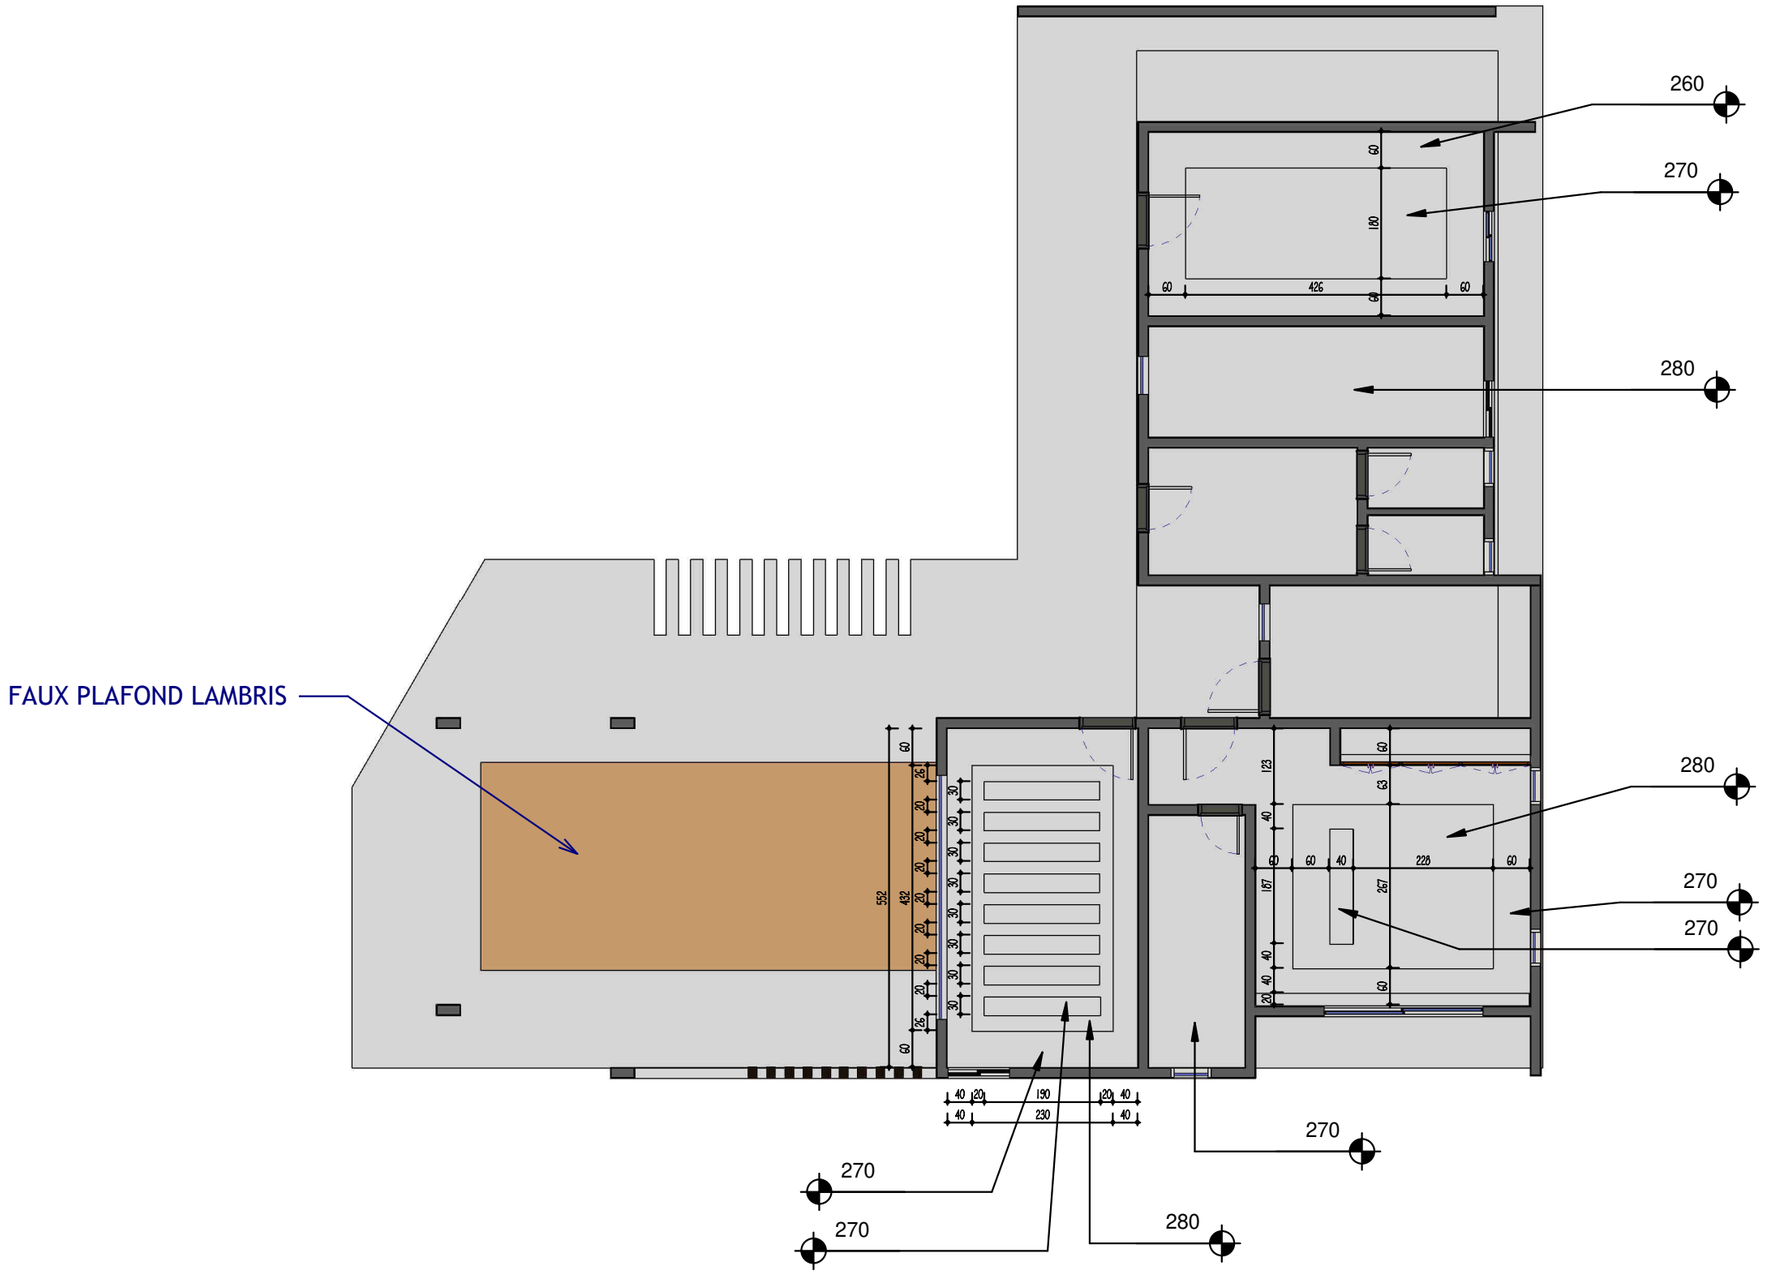


AFFAIRE:

MAITRE D'OEUVRE

EGARD

CHEF DE PROJET

ARTHUR EHOUNOUD

DESSIN

AUTEUR

PROJET

VILLA FOFIE

| AP | AP |
|---|---|
| D | S |

ECHELLE

1 : 100

PLAN N°

B 04

IMPRESSION

29/04/2021 20:06:21

PLAN PLAFOND TOITURE TERRASSE

MAITRE OUVRAGE

Lu et approuvé

MAITRE OEUVRE

Lu et approuvé

CE PROJET EST UNE PROPRIÉTÉ D'EGARD-ARCHITECTURE DESIGN. IL NE DOIT ÊTRE NI REPRODUIT NI MODIFIÉ SANS L'APPROBATION DU MAÎTRE D'OEUVRE. TOUTES MODIFICATIONS APPORTÉES AVEC OU SANS L'ACCORD DU MAÎTRE D'OEUVRE SUR LE PLAN OU SUR LE CHANTIER FERONT L'OBJET D'UN DEVIS SUPPLEMENTAIRE DONC FACTURÉES

COCODY-II PLTX-LAS PALMAS (CITE SICOGI BÂT K P124)
06 BP 535 ABJ 06, TEL: 22 01 48 75 / 22 42 06 48
FAX: 22 42 05 66, EMAIL: INFOS@EGARD-CI.COM

Sauvegardé dans: F:\PROJET EGARD 2020\4- VILLAS\FOFIE\VILLA FOFIE APS 6.rte