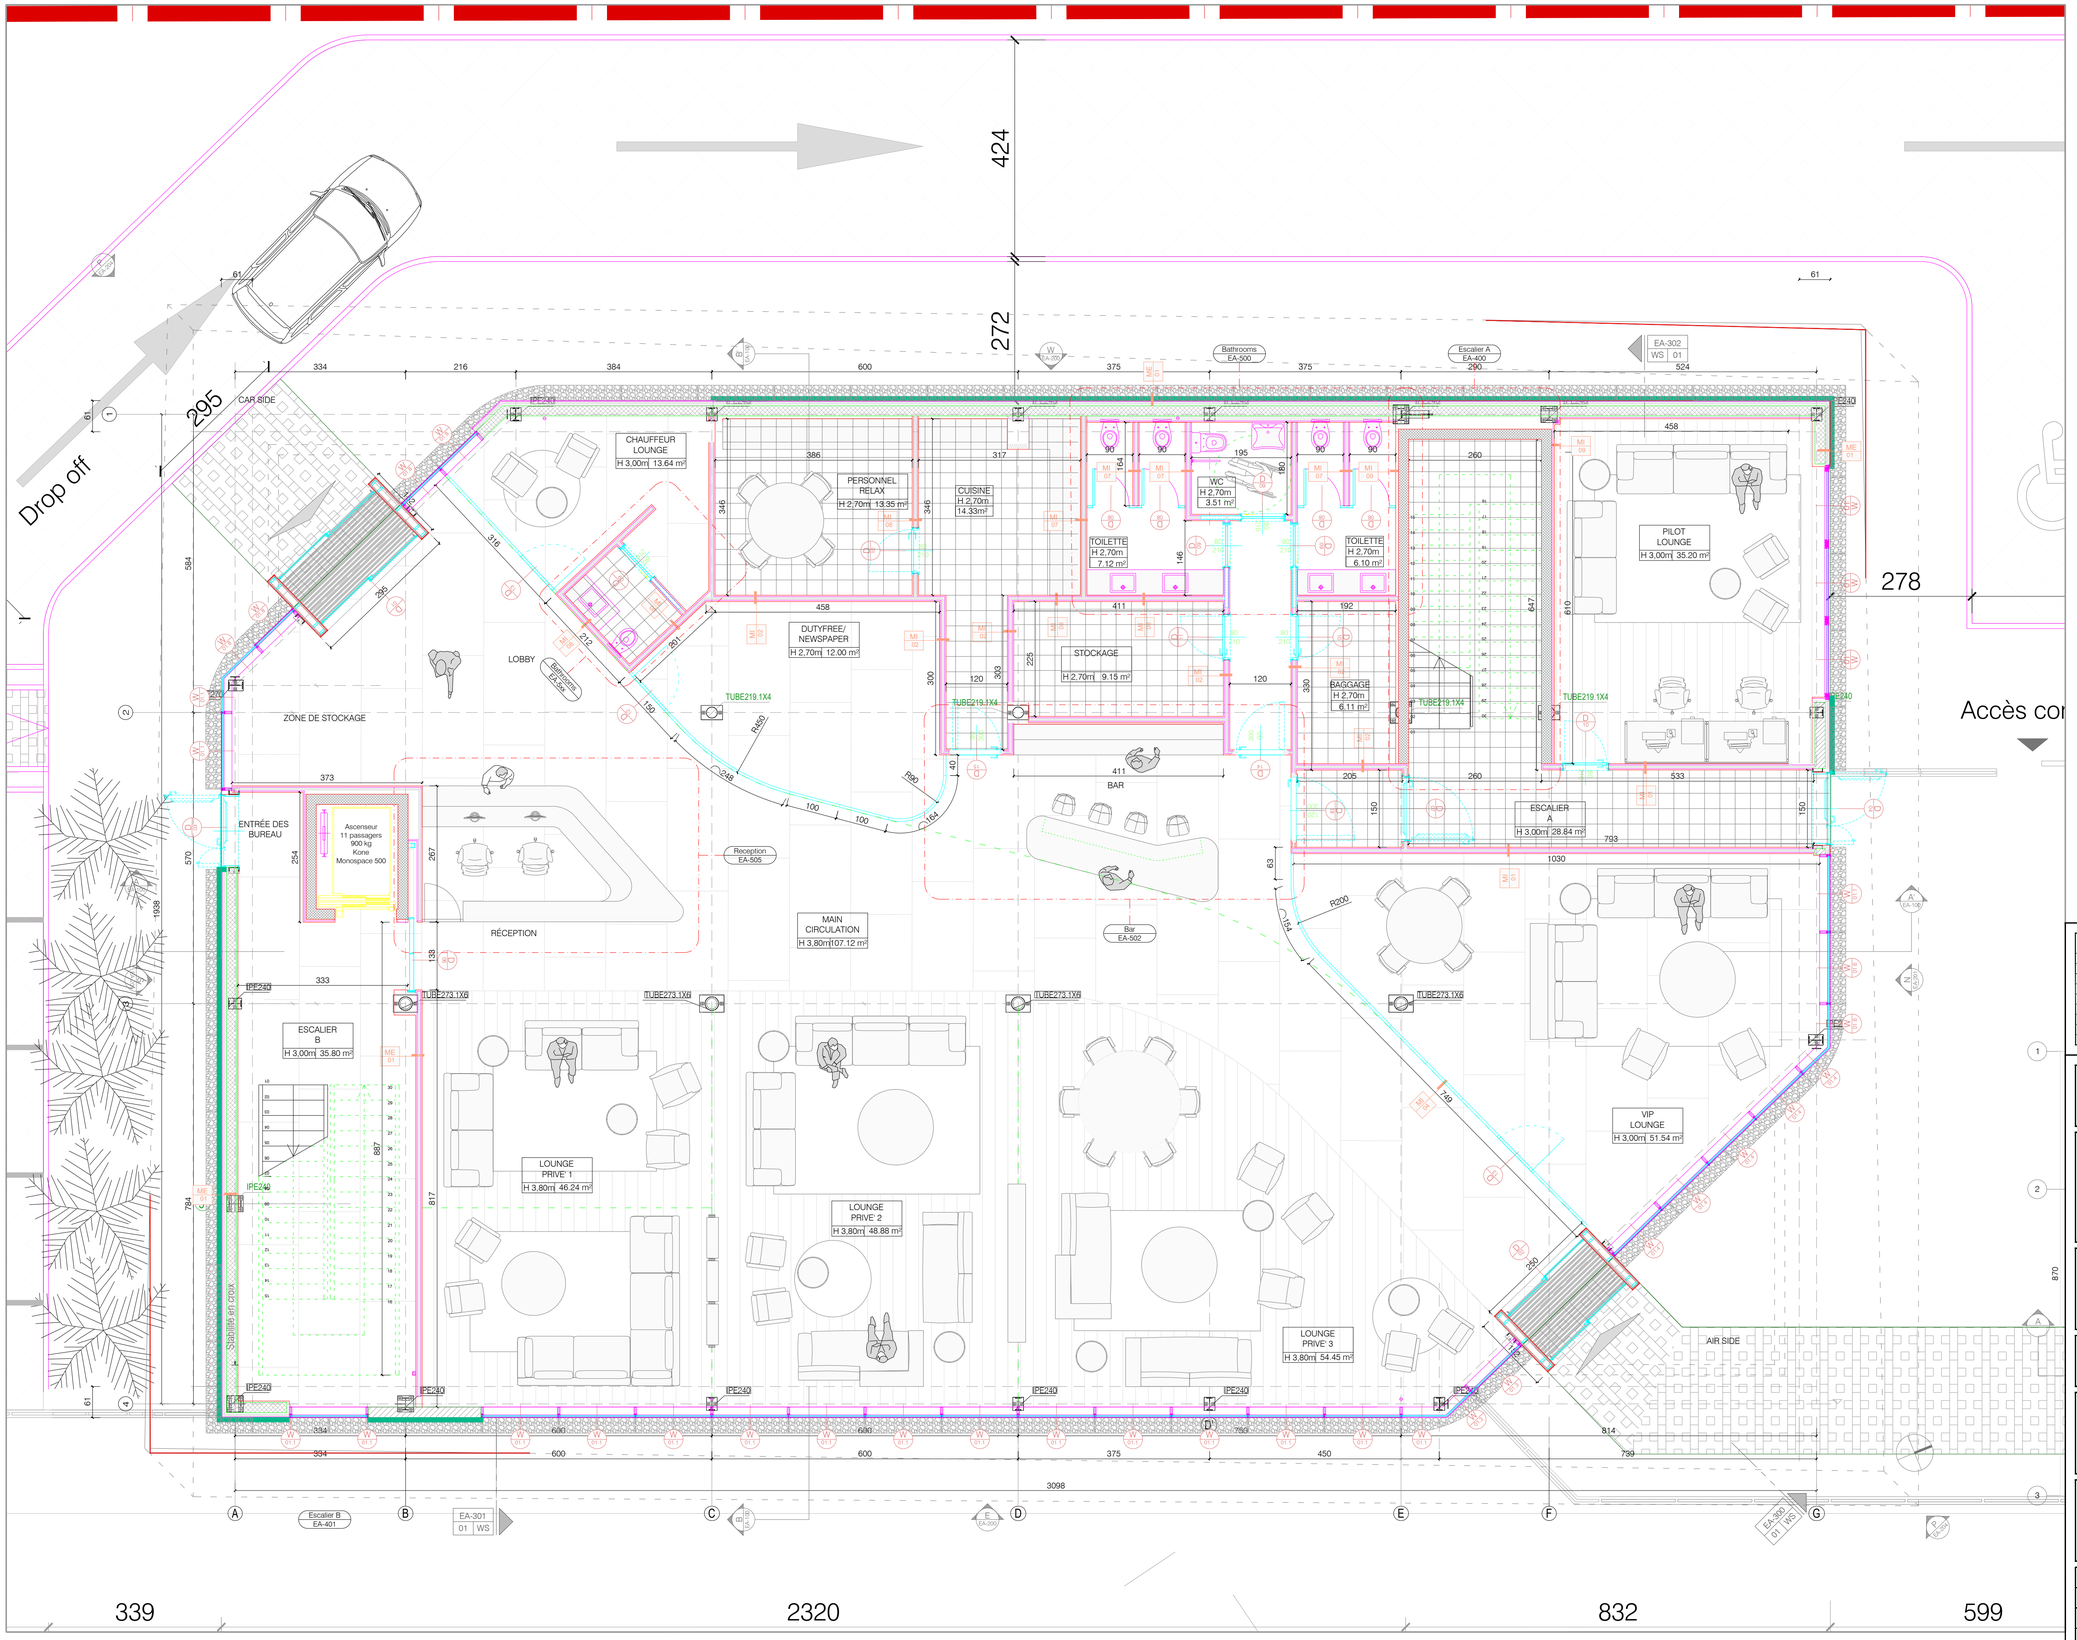


REZ DE CHAUSSEE

| MODIFICATIONS | | | | MODIFICATIONS | | | |
|---|---|---|---|---|---|---|---|
| DATE | IND / REV | TEXTE | PAR / BY | DATE | IND / REV | TEXTE | PAR / BY |
| 08/12/2016 | B | Optimisation des chuts techniques | OBT | -- | - | - | - |
| 07/04/2017 | E | Optimisation des chuts techniques | OBT | - | - | - | - |
| 24/04/2017 | F | Passage des poteux béton en poteaux métalliques | OBT | - | - | - | - |
| -- | - | - | - | -- | - | - | - |
| -- | - | - | - | -- | - | - | - |
SITE :

**ABIDJAN PORT BOUET**

PROJET :

CONSTRUCTION D'UN TERMINAL FBO

ABIDJAN PORT BOUET

MAÎTRE D'OUVRAGE :

**AERIA**

**PORT BOUET**
**ABIDJAN**
**TEL: 79 41 51 16**

ARCHITECTE :

BUREAU DE CONTROLE :

SOCOTEC AFRICA
Plateau-Rue du commerce,
Immeuble Amiral, 1er étage
01 BP 635 Abidjan 01
socotec.africa@i-socotec.org

SOCOTEC

MAÎTRE D'OEUVRE :

OBTIMA
GENERATEUR DE VALEUR

**Siège social :**

MARCORY CHAMPROUX
ABIDJAN
TEL: 79 41 51 16
E-mail : www.obtima.ci

TITRE :

**REZ DE CHAUSSEE**

| DESSINÉ PAR / DRAWN BY | APPROUVÉ PAR / APROVED BY | DATE | ÉCH/SCALE | FORMAT |
|---|---|---|---|---|
| OBTIMA | -- | **24.04.2017** | **1/60** | **A1** |

| N° D'AFFAIRE / JOB N° | PHASE / PHASE | LOT / WORK SECTION | NUMÉRO DE PLAN / DRAWING NUMBER | INDICE / REVISION |
|---|---|---|---|---|
| 0 1 0 1 | M A R | A R C | - 0 0 2 | – F |