


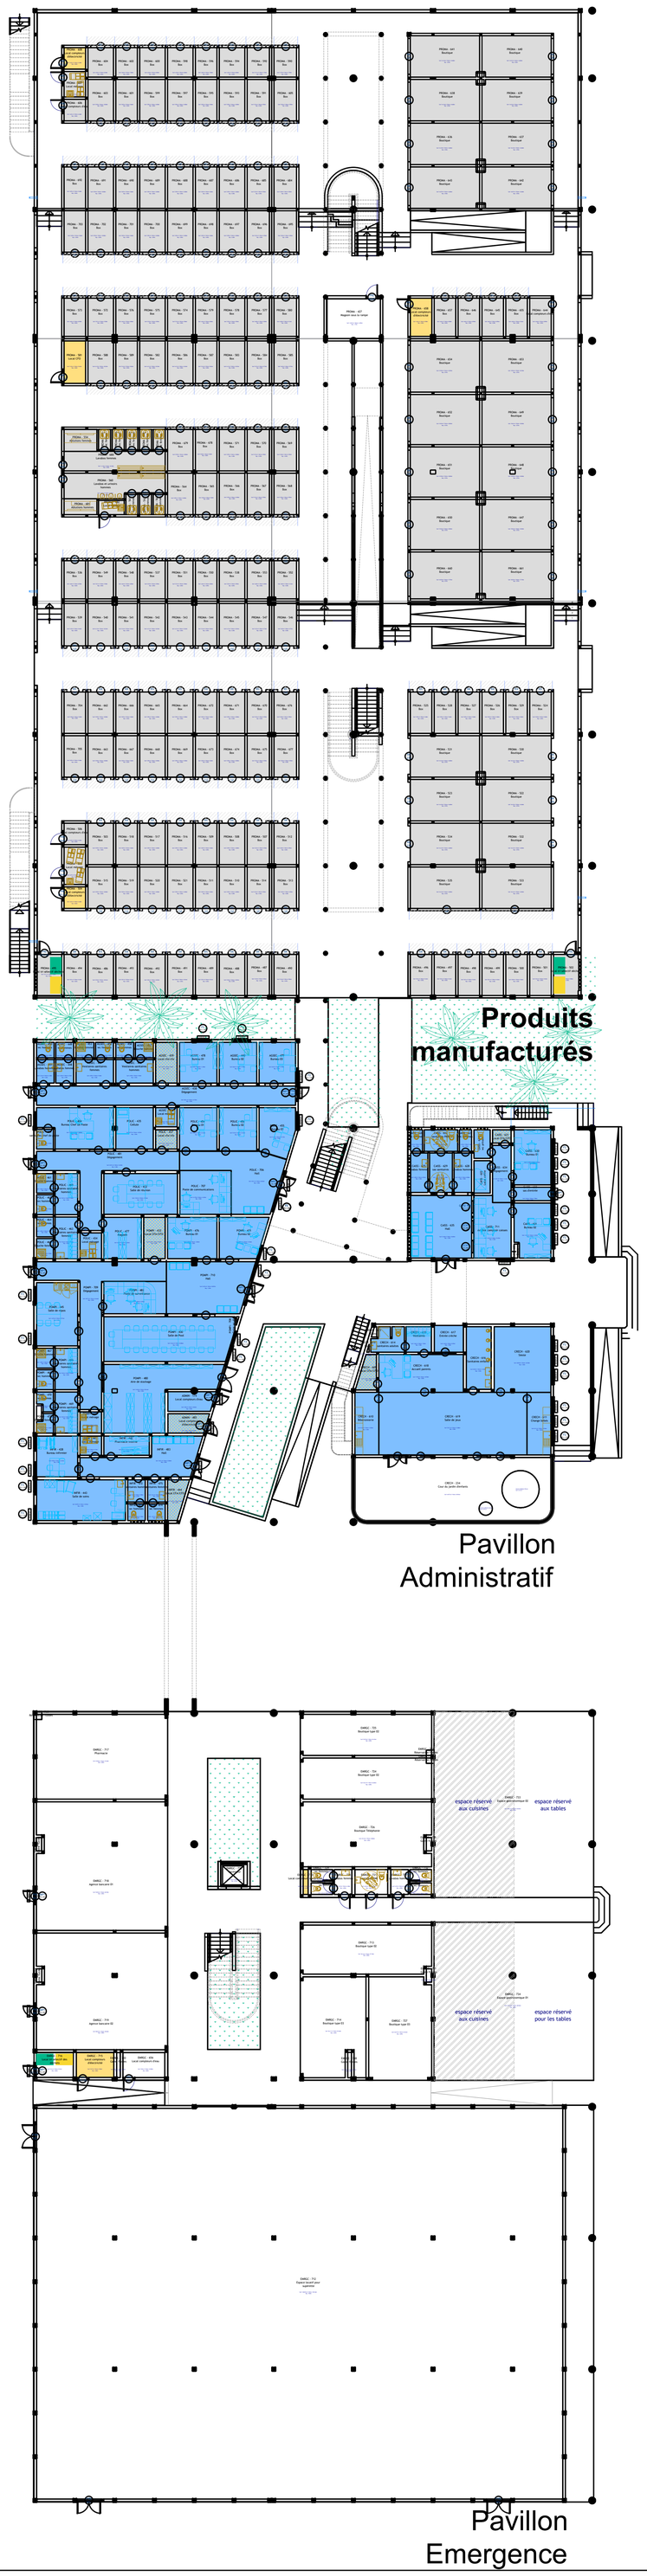


**LEGENDE PLAFONDS**

**NB: les espaces laissés sans designation de plafonds sont laissés brut et seront à la charge du preneur des lieux pour les pièces avec une dalle, ou bien sont couverts avec une charpente & couverture.**

**Cf plan de structures pour repérage des dalles et charpentes**

- ENDUIT DE CIMENT SOUS PLAFOND
- ENDUIT DE PLATRE SOUS PLAFOND
- PLAFOND DEMONTABLE 60x60
- PLAFOND EN CONTREPLAQUE
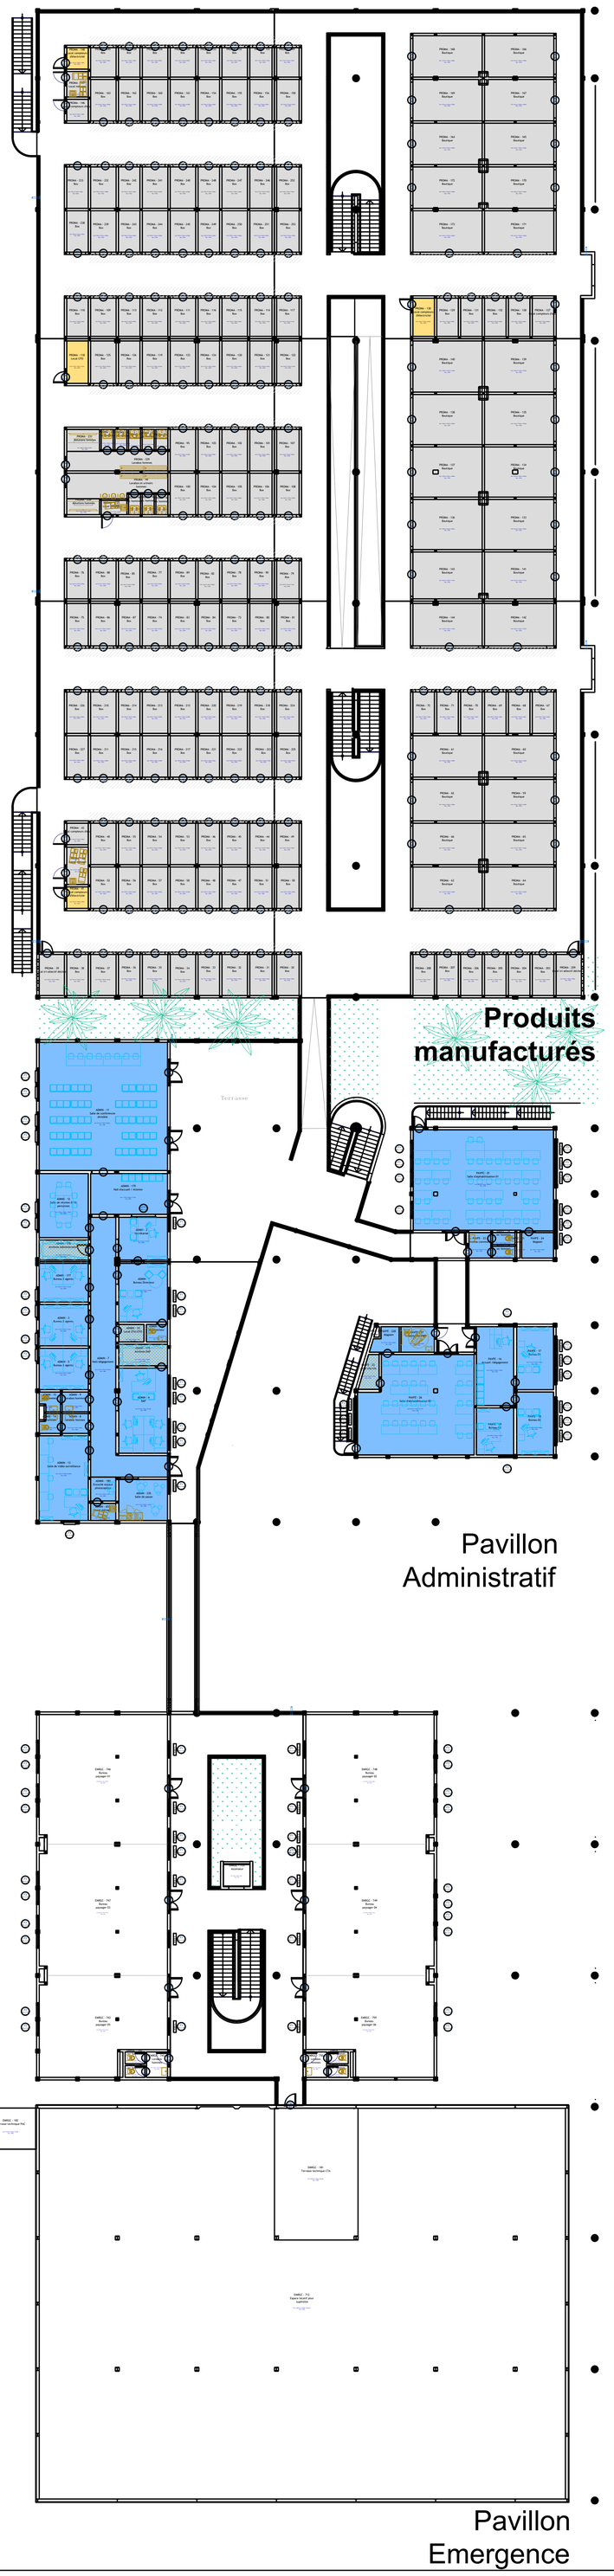
| Rev | Date | Sommaire des modification | Dessiné par | Verifié par | Approuvé par |
|---|---|---|---|---|---|
| C | 01/2022 | Mise à jour DCE | | | |
| B | 06/2021 | Mise à jour | | | |
| A | 12/2020 | Emission d'origine | | | |

REPUBLIQUE DE COTE D'IVOIRE

Union- Discipline- Travail

**Bailleur de fonds:**

**Agence Française de Développement**
Bd F.Mitterand- Cocody- Université
01 BP 1814- Abidjan- Côte d'Ivoire
Tél: +225 22 40 70 40- Fax: +225 22 44 21 78
E-mail: afdabidjan@afd.fr

**Maître d'Ouvrage:**

**MAIRIE DE YOPOUGON**
Quartier de Yopougon- SELMER
Boîte Postale 21 BP Abidjan 21
Côte d'Ivoire
Télécopie: +225 23 45 16 75- E-mail: kafangilbert@gmail.com

**Assistants au Maître d'Ouvrage:**

**ARTELIA**
Rue des Papayes- Cocody Mermoz- Abidjan- Côte d'Ivoire- Tél: +225 54 16 10 08- Email: contact@ci.artelia group.com

**CAURIS ARCHITECTURE**
25 BP 2030, Riviera Golf 1, à côté de Lycée Maurice Delafosse- Abidjan- Côte d'Ivoire- Tél: +225 27 22 43 61 30- Email: caurisabidjan@cauris.net

**2D CONSULTING AFRIQUE**
Pharmacie Saint Pierre des Rosées, Villa n°L8, Cité Belle Vue- Riviera 3- Cocody- 15 BP 149 Abidjan 15- Abidjan-Côte d'Ivoire- Tél: +225 07 49 40 01 59

**Prestataire de Service:**

**Le Groupement COMETE International / SCO Afrique de l'Ouest**

**COMETE INTERNATIONAL**
1082 Tunis Mahrajène- BP 97 Tunis- 1002 Tunisie
Tél: (+216) 71 70 78 00-71 70 79 00- Fax: (+216) 71 70 72 00
E-mail: dg@comete.com.tn- Site Web: www.comete-group.com

**SCO AFRIQUE DE L'OUEST**
01 PB 4097 Abidjan 01- Côte d'Ivoire
Tél: (+225) 20 21 66 30/ 20 21 28 82- Fax: (+225) 21 85 90
E-mail: direction.generale@scoao.ci

VISA

**Architectes:**

***PHASE ESQ/APS:***
**SKY ARCHITECTES**
29 Boulevard Clozel- Plateau- 06 BP 1971 Abidjan 06- Côte d'Ivoire-
Tél: +225 20 21 32 48- +225 20 21 32 92.

***PHASE APD/PRO/DCE/PERMIS DE CONSTRUIRE:*** **SEA SUARL - JOHN K.P. RYAN,** Architecte D.P.L.G.
11 rue El Hijaz, 1002, Tunis Belvédère
Tél: (+216) 22 592 037 - Email: jpkryan@yahoo.fr
**CREATIV'LAB**
Cocody Palmeraie Akuedo- 21 BP 2020 Abidjan 21- Côte d'Ivoire Tél: (+216) 05 05 84 11 38 - Email: creativlab.architectes@gmail.com

VISA

**Projet:**

# CONSTRUCTION DU MARCHE DE DEMI-GROS ET DE DETAIL DE LA COMMUNE DE YOPOUGON

**Bâtiment:** MARCHE DE DETAIL

PAVILLONS EMERGENCE ET ADMINISTRATION, PRODUITS MANUFACTURES

**Titre du plan:**

## PLAN DE REPERAGE DES PLAFONDS

| Format : A0 | Echelle : 1 : 200 | Nom du fichier source: C:\Users\John K.P. RYAN\Documents\[18097] Marché de Yopougon\05 - DCE\DCE PLANS\MADDY_MARCHE_DETAIL.rvt |
|---|---|---|

| 18097 | DCE | MADDY | MADDY | ARC | 601 | C |
|---|---|---|---|---|---|---|
| Numéro d'affaire | Phase | Projet | Découpage | Discipline | Numéro du plan | Indice |