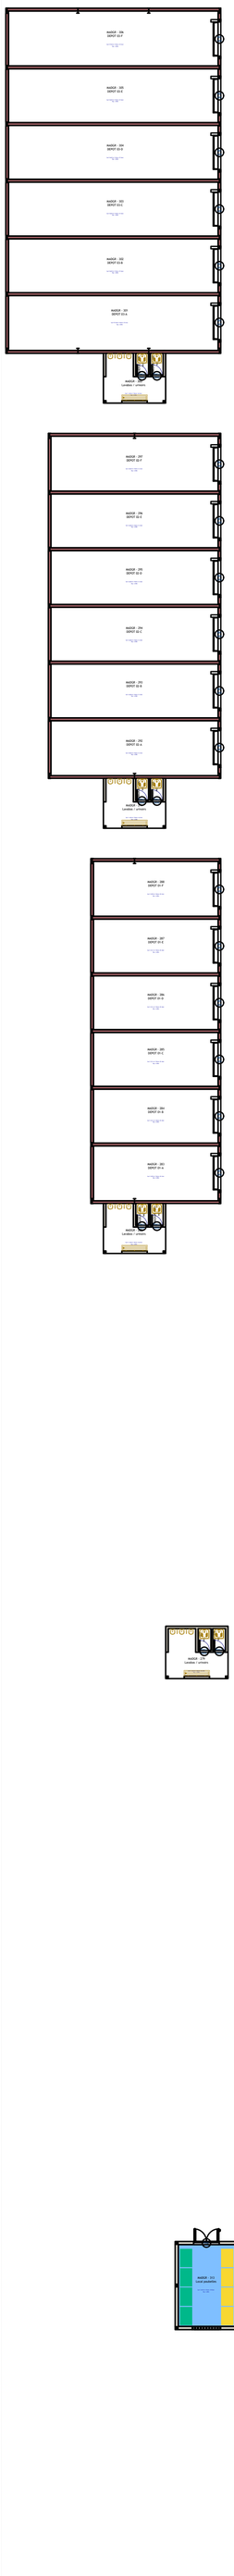

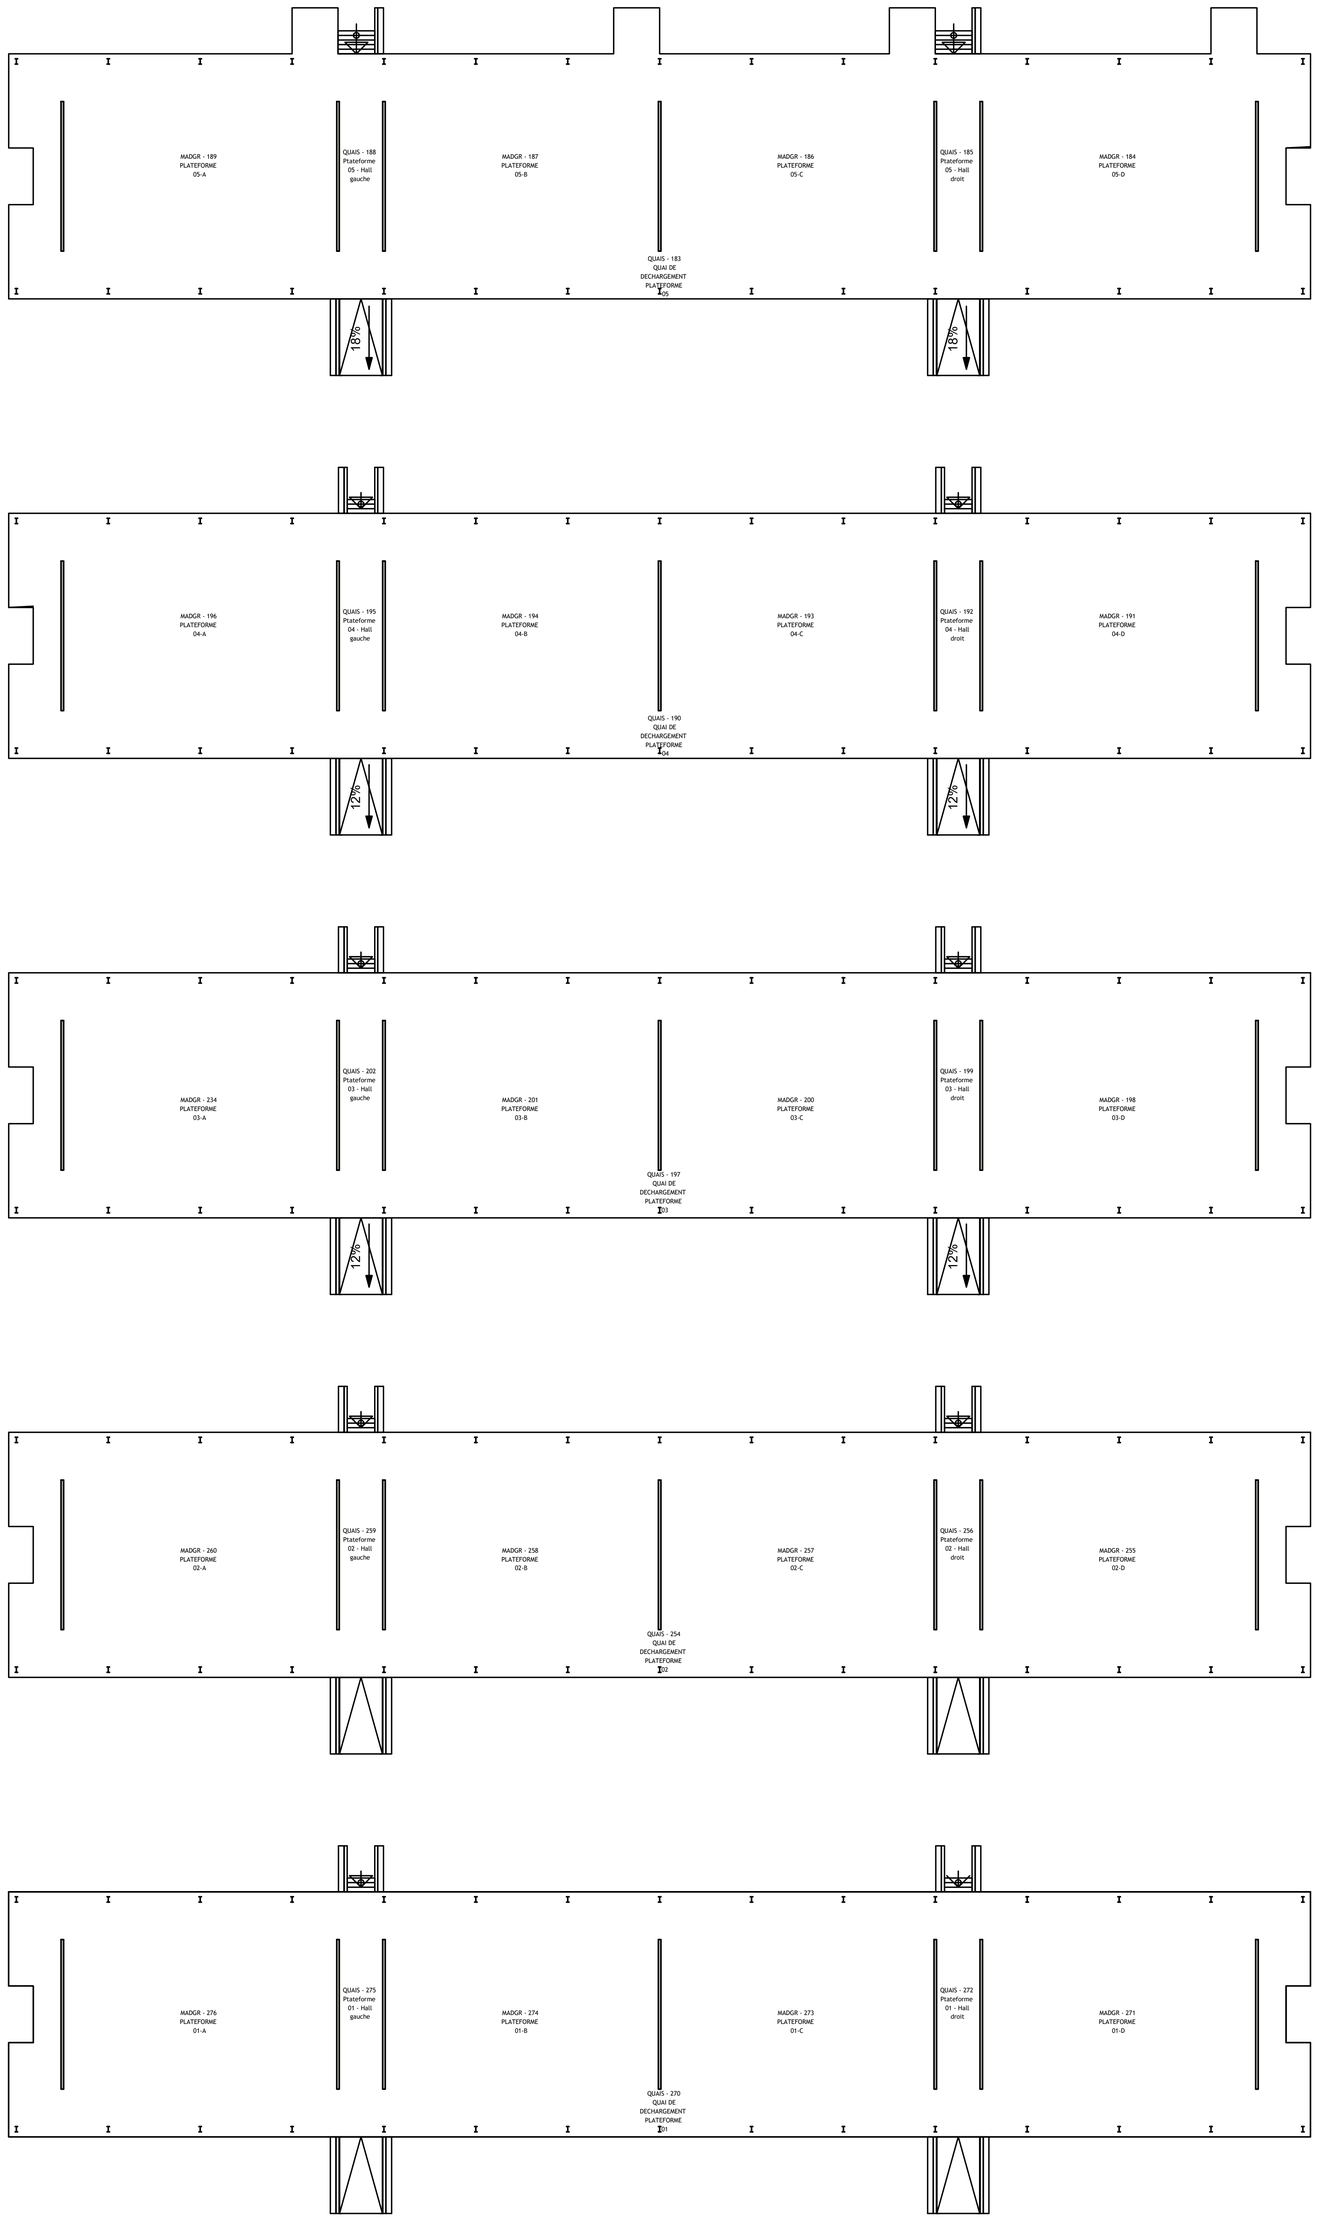

LEGENDE PLAFONDS

NB: les espaces laissés sans designation de plafonds sont laissés brut et seront à la charge du preneur des lieux pour les pièces avec une dalle. ou bien sont couverts avec une charpente & couverture.

Cf plan de structures pour repérage des dalles et charpentes

- ENDUIT DE CIMENT SOUS PLAFOND
- ENDUIT DE PLATRE SOUS PLAFOND
- PLAFOND DEMONTABLE 60x60
- PLAFOND EN CONTREPLAQUE

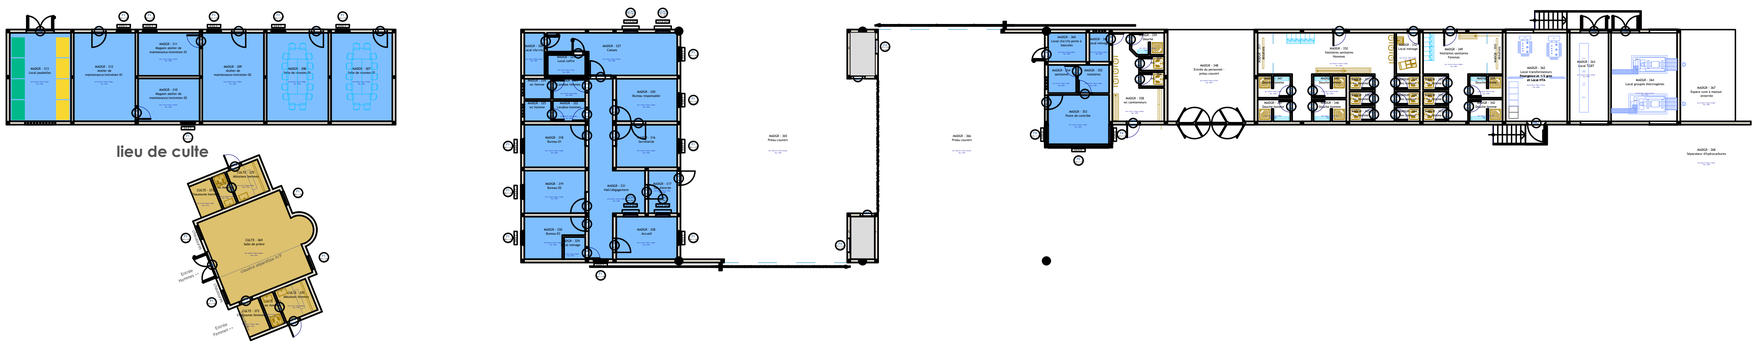

Rev	Date	Sommaire des modification	Dessiné par	Verifié par	Approuvé par
C	01/2022	Mise à jour DCE			
B	06/2021	Mise à jour			
A	12/2020	Emission d'origine			

REPUBLIQUE DE COTE D'IVOIRE

Union- Discipline- Travail

Bailleur de fonds:

Agence Française de Développement
Bd F.Mitterand- Cocody- Université
01 BP 1814- Abidjan- Côte d'Ivoire
Tél: +225 22 40 70 40- Fax: +225 22 44 21 78
E-mail: afdabidjan@afd.fr

Maître d'Ouvrage:

MAIRIE DE YOPOUGON
Quartier de Yopougon- SELMER
Boîte Postale 21 BP Abidjan 21
Côte d'Ivoire
Télécopie: +225 23 45 16 75- E-mail: kafangilbert@gmail.com

Assistants au Maître d'Ouvrage:

ARTELIA
Rue des Papayes- Cocody Mermoz- Abidjan- Côte d'Ivoire- Tél: +225 54 16 10 08- Email: contact@ci.artelia group.com

CAURIS ARCHITECTURE
25 BP 2030, Riviera Golf 1, à côté de Lycée Maurice Delafosse- Abidjan- Côte d'Ivoire- Tél: +225 27 22 43 61 30- Email: caurisabidjan@cauris.net

2D CONSULTING AFRIQUE
Pharmacie Saint Pierre des Rosées, Villa n°L8, Cité Belle Vue- Riviera 3- Cocody- 15 BP 149 Abidjan 15- Abidjan-Côte d'Ivoire- Tél: +225 07 49 40 01 59

Prestataire de Service:

Le Groupement COMETE International / SCO Afrique de l'Ouest

COMETE INTERNATIONAL
1082 Tunis Mahrajène- BP 97 Tunis- 1002 Tunisie
Tél: (+216) 71 70 78 00-71 70 79 00- Fax: (+216) 71 70 72 00
E-mail: dg@comete.com.tn- Site Web: www.comete-group.com

SCO AFRIQUE DE L'OUEST
01 PB 4097 Abidjan 01- Côte d'Ivoire
Tél: (+225) 20 21 66 30/ 20 21 28 82- Fax: (+225) 21 85 90
E-mail: direction.generale@scoao.ci

VISA

Architectes:

PHASE ESQ/APS:
SKY ARCHITECTES
29 Boulevard Clozel- Plateau- 06 BP 1971 Abidjan 06- Côte d'Ivoire-
Tél: +225 20 21 32 48- +225 20 21 32 92.

PHASE APD/PRO/DCE/PERMIS DE CONSTRUIRE: **SEA SUARL - JOHN K.P. RYAN,** Architecte D.P.L.G.
11 rue El Hijaz, 1002, Tunis Belvédère
Tél: (+216) 22 592 037 - Email: jpkryan@yahoo.fr
CREATIV'LAB
Cocody Palmeraie Akuedo- 21 BP 2020 Abidjan 21- Côte d'Ivoire Tél: (+216) 05 05 84 11 38 - Email: creativlab.architectes@gmail.com

VISA

Projet:

CONSTRUCTION DU MARCHE DE DEMI-GROS ET DE DETAIL DE LA COMMUNE DE YOPOUGON

Bâtiment:

MARCHE DE DEMI-GROS

Titre du plan:

PLAN DE REPERAGE DES PLAFONDS

Format : A0	Echelle : 1 : 200	Nom du fichier source:	C:\Users\John K.P. RYAN\Documents\18097\ Marché de Yopougon\05 - DCE\DCE PLANS\MADDY_MARCHE_DETAIL.rvt

18097	DCE	MADDY	MADDY	ARC	600	C
Numéro d'affaire	Phase	Projet	Découpage	Discipline	Numéro du plan	Indice