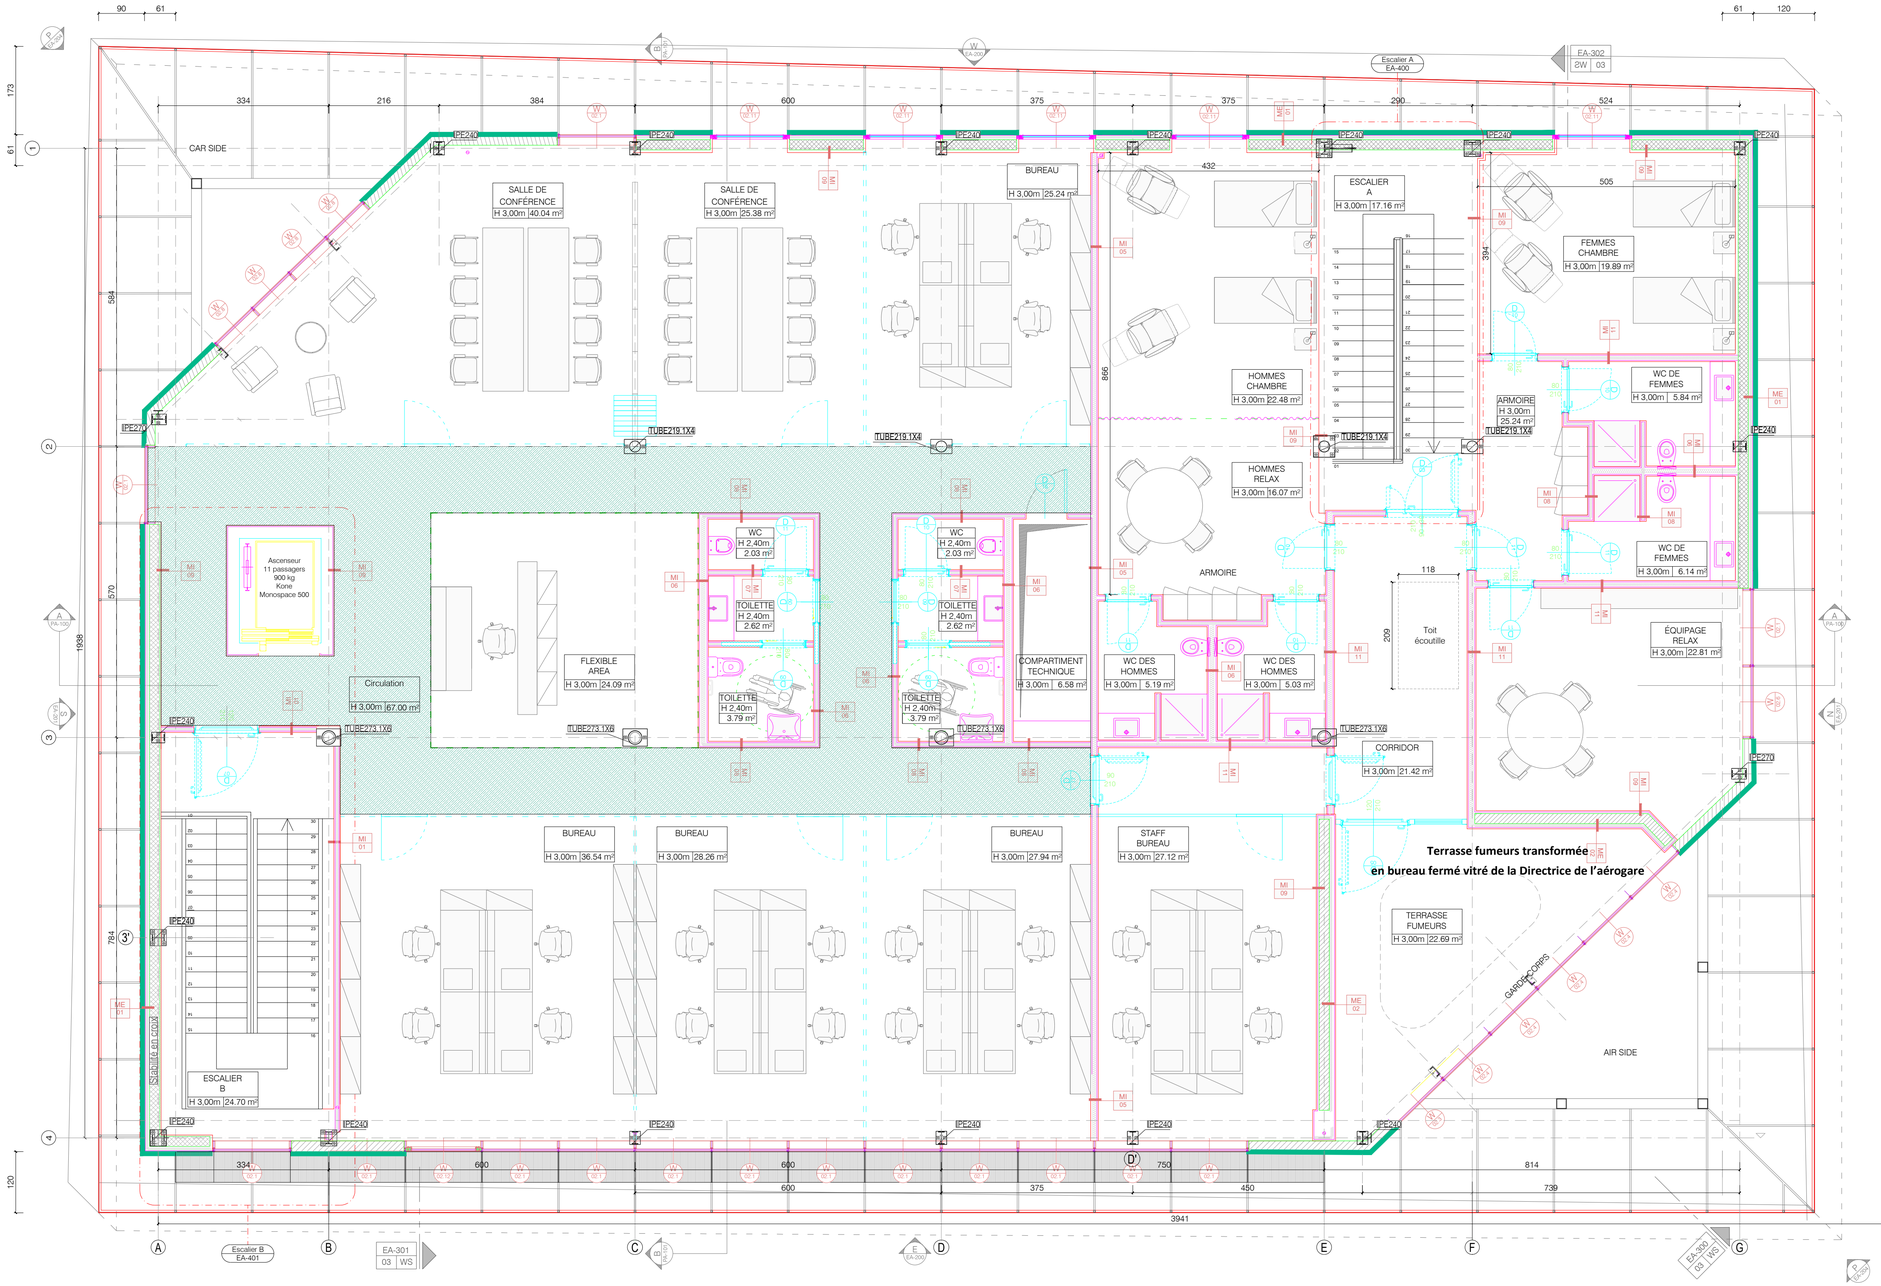

FIRST FLOOR

PREMIER ÉTAGE

MODIFICATIONS				MODIFICATIONS			
DATE	IND. REV.	TEXTE	PAR BY	DATE	IND. REV.	TEXTE	PAR BY
01/12/2016	B	Optimisation des choix techniques	OBT	"	"	.	"
22/03/2017	C	Optimisation des choix techniques	OBT	"	"	.	"
07/04/2017	D	Optimisation des choix techniques	OBT	"	"	.	"
24/04/2017	E	Passage des poteaux béton en poteaux métalliques	OBT	"	"	.	"
"	"	.	"	"	"	.	"
"	"	.	"	"	"	.	"
"	"	.	"	"	"	.	"
"	"	.	"	"	"	.	"

SITE :

ABIDJAN PORT BOUET

PROJET :

CONSTRUCTION D'UN TERMINAL FBO

ABIDJAN PORT BOUET

AERIA

MAÎTRE D'OUVRAGE :

AERIA

PORT BOUET
ABIDJAN
TEL: 79 41 51 16

ARCHITECTE :

BUREAU DE CONTROLE :

SOCOTEC AFRICA
Plateau Rue du commerce,
Immeuble Amiral, 1er étage
01 BP 635 Abidjan 01
socotec.africa@-socotec.org

SOCOTEC

MAÎTRE D'OEUVRE :

OBTIMA
GENERATEUR DE VALEUR

Siège social :

MARCORY CHAMPROUX
ABIDJAN
TEL : 79 41 51 16
E-mail : www.obtima.ci

TITRE :

ETAGE

DESSINÉ PAR DRAWN BY	APPROUVÉ PAR APROVED BY	DATE	ÉCHSCALE	FORMAT
OBTIMA	"	05.04.2017	1/60	A1

N° D'AFFAIRE JOB N°	PHASE PHASE	LOT WORK SECTION	NUMÉRO DE PLAN DRAWING NUMBER	INDICE REVISION
0 1 0 1	M A R	A R C	- 0 0 3	– D