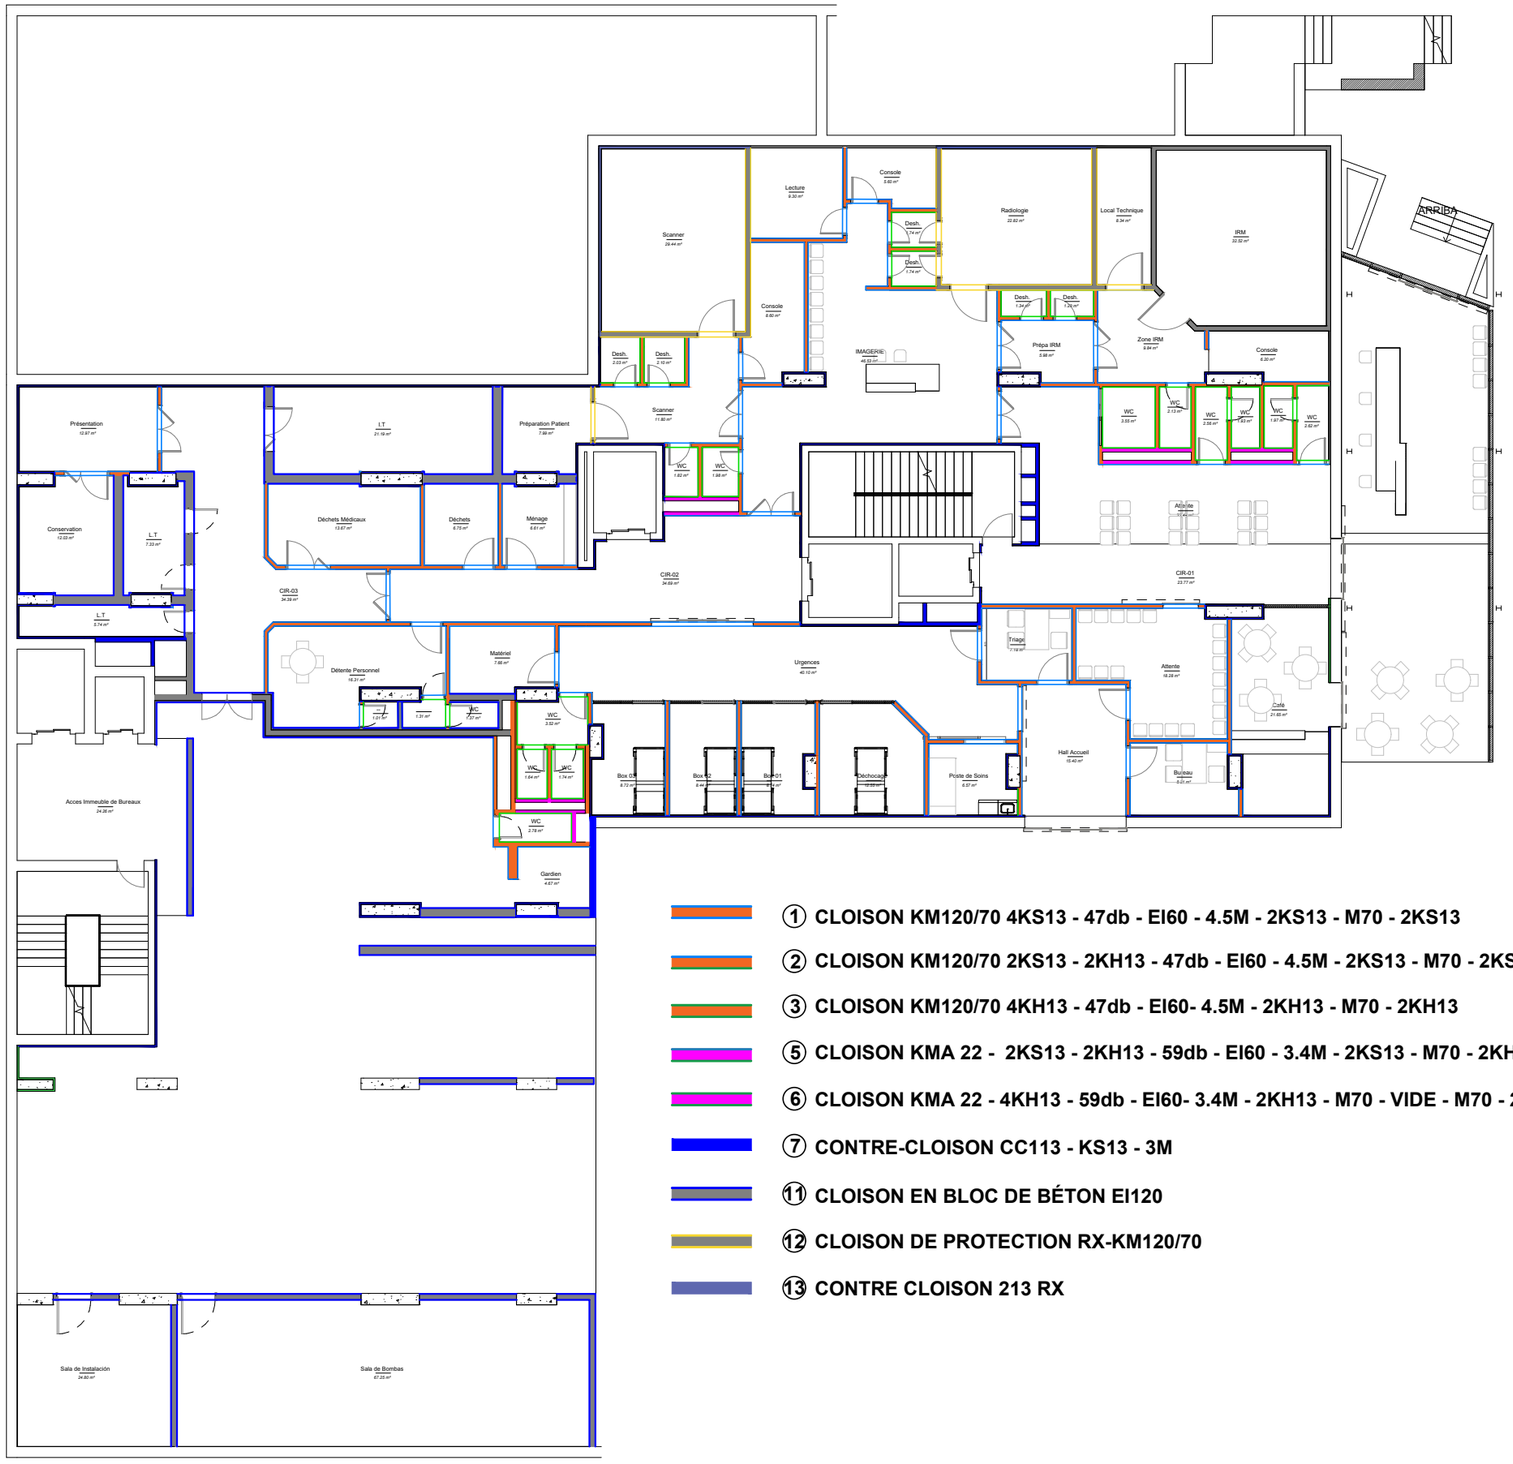

① CLOISON KM120/70 4KS13 - 47db - EI60 - 4.5M - 2KS13 - M70 - 2KS13

② CLOISON KM120/70 2KS13 - 2KH13 - 47db - EI60 - 4.5M - 2KS13 - M70 - 2KS13

③ CLOISON KM120/70 4KH13 - 47db - EI60- 4.5M - 2KH13 - M70 - 2KH13

⑤ CLOISON KMA 22 - 2KS13 - 2KH13 - 59db - EI60 - 3.4M - 2KS13 - M70 - 2KH13

⑥ CLOISON KMA 22 - 4KH13 - 59db - EI60- 3.4M - 2KH13 - M70 - VIDE - M70 - 2KH13

⑦ CONTRE-CLOISON CC113 - KS13 - 3M

⑪ CLOISON EN BLOC DE BÉTON EI120

⑫ CLOISON DE PROTECTION RX-KM120/70

⑬ CONTRE CLOISON 213 RX

MAITRE D'OEUVRE: Design Engineering Solutions	***CLINIQUE GOUMIN***	DATE 16/02/2023	FORMAT PAPIER: A3
PHASE: **A P D**	***PS4***	ECHELLE: 1:200	CODE: 00-DES22.02GOU