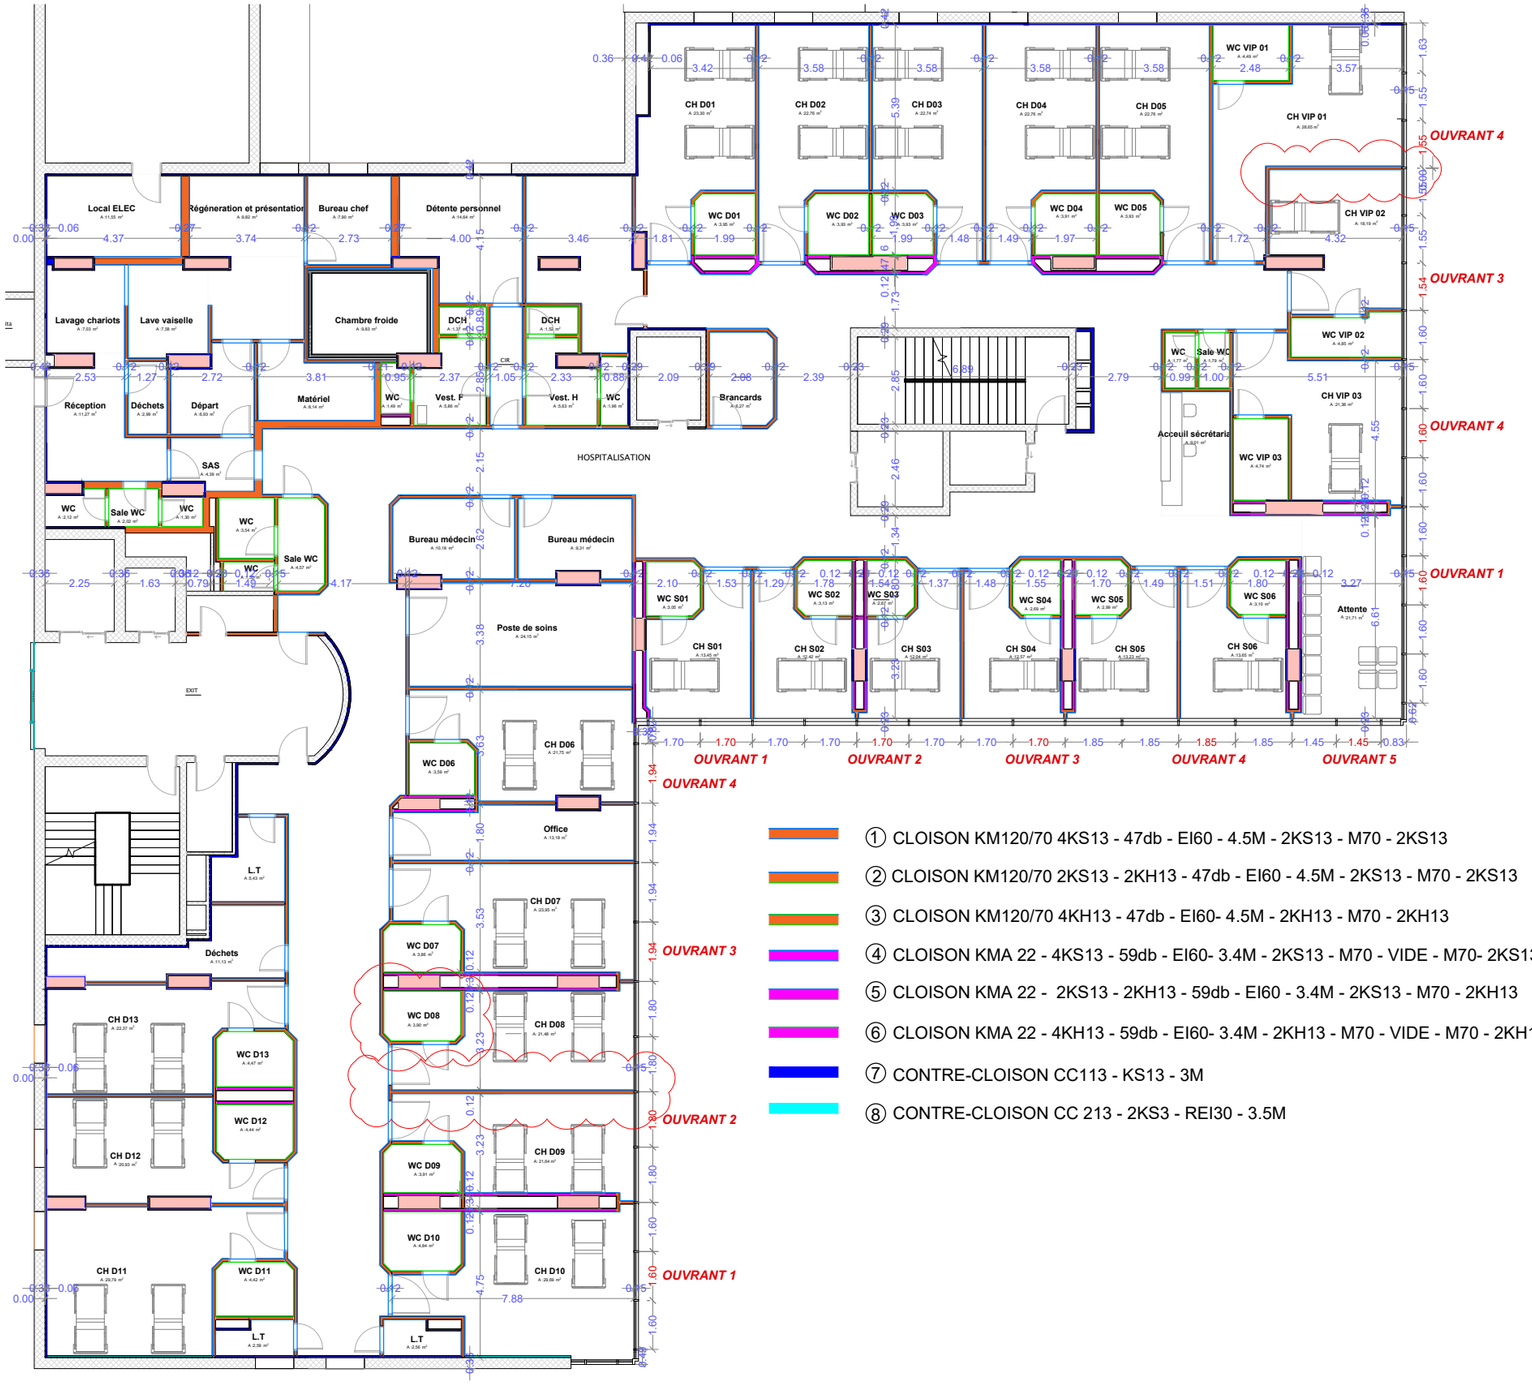

① CLOISON KM120/70 4KS13 - 47db - EI60 - 4.5M - 2KS13 - M70 - 2KS13

② CLOISON KM120/70 2KS13 - 2KH13 - 47db - EI60 - 4.5M - 2KS13 - M70 - 2KS13

③ CLOISON KM120/70 4KH13 - 47db - EI60- 4.5M - 2KH13 - M70 - 2KH13

④ CLOISON KMA 22 - 4KS13 - 59db - EI60- 3.4M - 2KS13 - M70 - VIDE - M70- 2KS13

⑤ CLOISON KMA 22 - 2KS13 - 2KH13 - 59db - EI60 - 3.4M - 2KS13 - M70 - 2KH13

⑥ CLOISON KMA 22 - 4KH13 - 59db - EI60- 3.4M - 2KH13 - M70 - VIDE - M70 - 2KH13

⑦ CONTRE-CLOISON CC113 - KS13 - 3M

⑧ CONTRE-CLOISON CC 213 - 2KS3 - REI30 - 3.5M

ARCHITECTE PROJET :	PHASE: **A P D**	***PROJET CLINIQUE GOUMIN RDC/P0: HOSPITALISATIONS***	DATE 28/02/2023	FORMAT PAPIER: A3
Missing or invalid reference File: ../../../../00-HCI - Cred/02_ PRESENTATIONS/01_AMO MOE/[illegible]/LBDD_HCI.pdf.pdf Sheet: 1	ARCHITECTE : Nancy MELEDJE		ECHELLE: 1:200	CODE: 00-DES22.02GOU